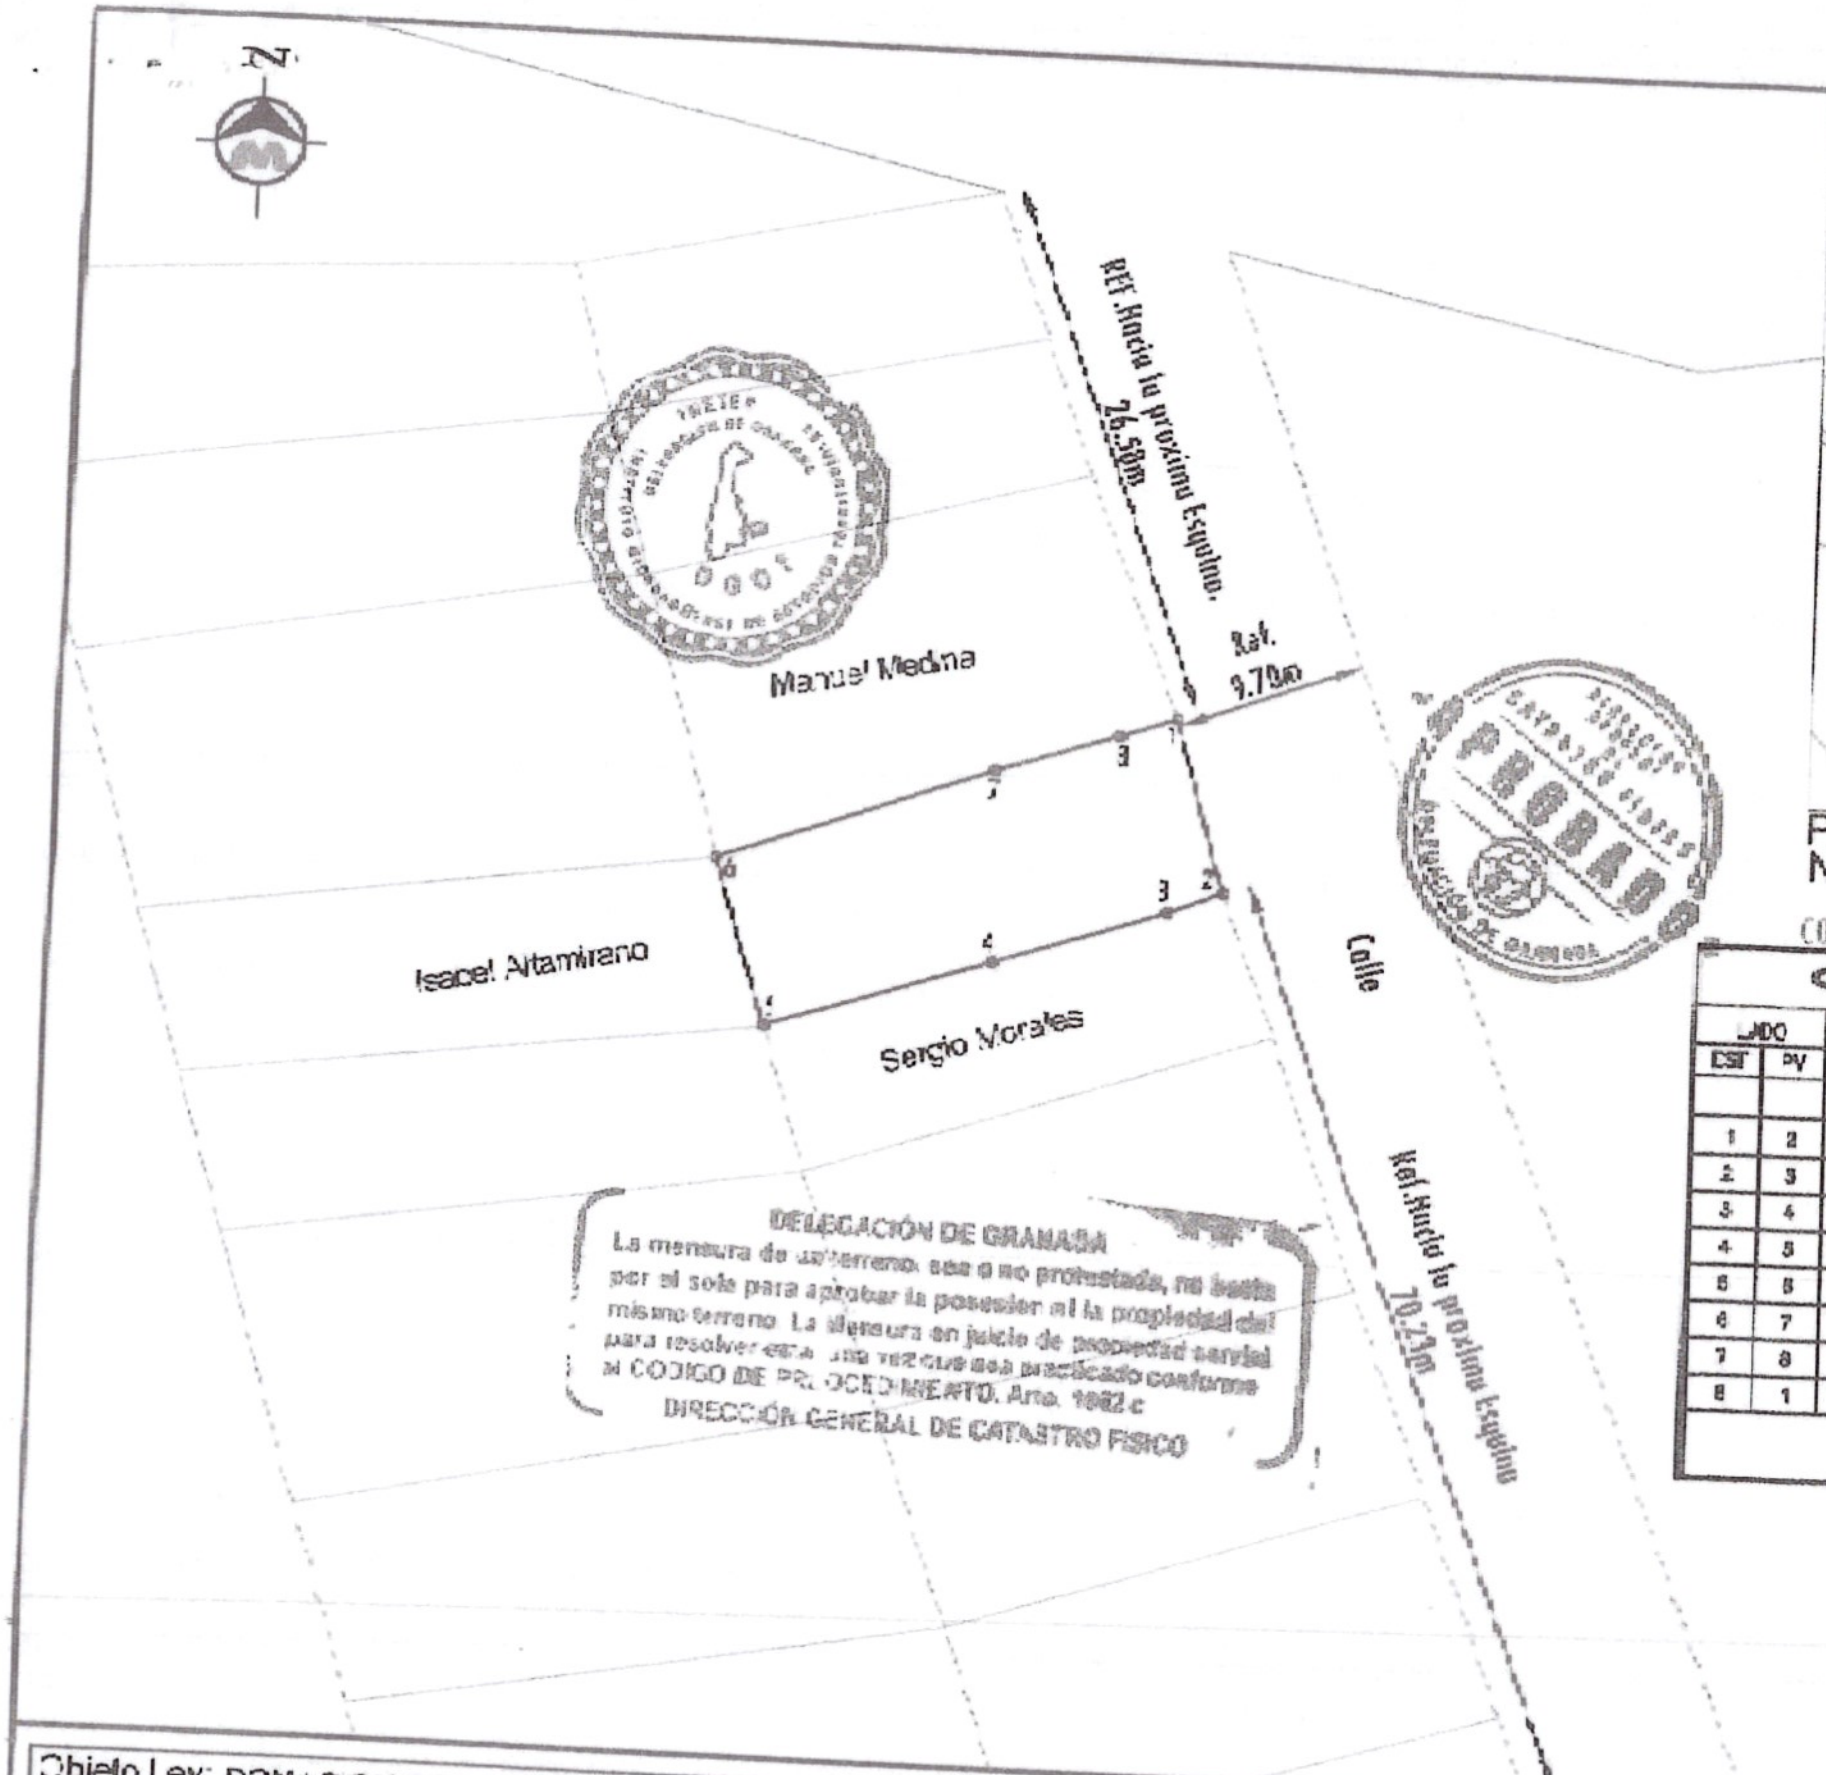

DEPARTAMENTO DE GRANADA MUNICIPIO DE NANDAIME

Planta de Ubicacion Sin Escala
Número Catastral:2951-2-08-000-(18500)

COORDENADAS NO VINCULADAS A LA RED GEODESICA DE NICARAGUA

CUADRO DE CONSTRUCCION

LADO EST	LADO PV	RUMBO	DISTANCIA	V	COORDENADAS Y	COORDENADAS X
				1	1,300,245.3138	604491.1 881
1	2	S 17° 725.26" E	8.940	2	1,300,236.7778	604493.5251
2	3	S 88°2202.12" W	2.965	3	1,300,235.6848	604491.0891
3	4	S 72°0251.29" W	9.162	4	1,300,232.8608	604482.3531
4	5	S 72°0539.43" W	11.944	5	1,300,229.1851	604470.9983
5	6	N 18°4540.41" W	8.653	6	1,300,237.3762	604468.1 980
6	7	N 70° 515.19" E	14.749	7	1,300,242.3592	604482.0800
7	8	N 72°0212.32" E	6.428	8	1,300,244.3418	604488.1 951
8	1	N 71°5342.44" E	3.128	1	1,300,245.3138	604491.1 881

SUPERFICIE = 216.861 m2

Objeto Lev: DONACION DE MITAD INDIVISA	Numero Catastral: 2951-2-08-000-(18500)	Fecha: 14 de octubre del 2025	FIRMA:
Enajenante: Rosa Alfredina Medina Blanco ced:202-140552-0001U	Ubicación: REPTO JAVIER GUERRA, II ETAPA CASA N° 133 Municipio de Nandaime, Dpto Granada	Ejecuta: Ing. Bosco Javier Morgan L.C. Catastral: BMM100426 Cel: 8883-7588 Email: ingmorgan73@gmail.com servicios topograficos	
Acquiere: Karina Rebeka Bonilla Medina ced:001-101288-0059D	Área: 216.861 m2 = 307.599Vrs2	Escala: 1 / 500	

MORGAN Servicios Topograficos Ing. Bosco Javier Morgan L.C. Catastral Cel: 8883-7588

Transacción	Cudoc	Objeto Plano	Área (m²)	No. Lote
T-46FII5-001	0039339	DESMEMBRACION	216.86	
Parcela Objeto	63002042738128		Documento	
No. Licencia: BMM100426	Fecha Aprobación: 10/11/2025		Fecha Vencimiento: 10/11/2026	W8BYVHK