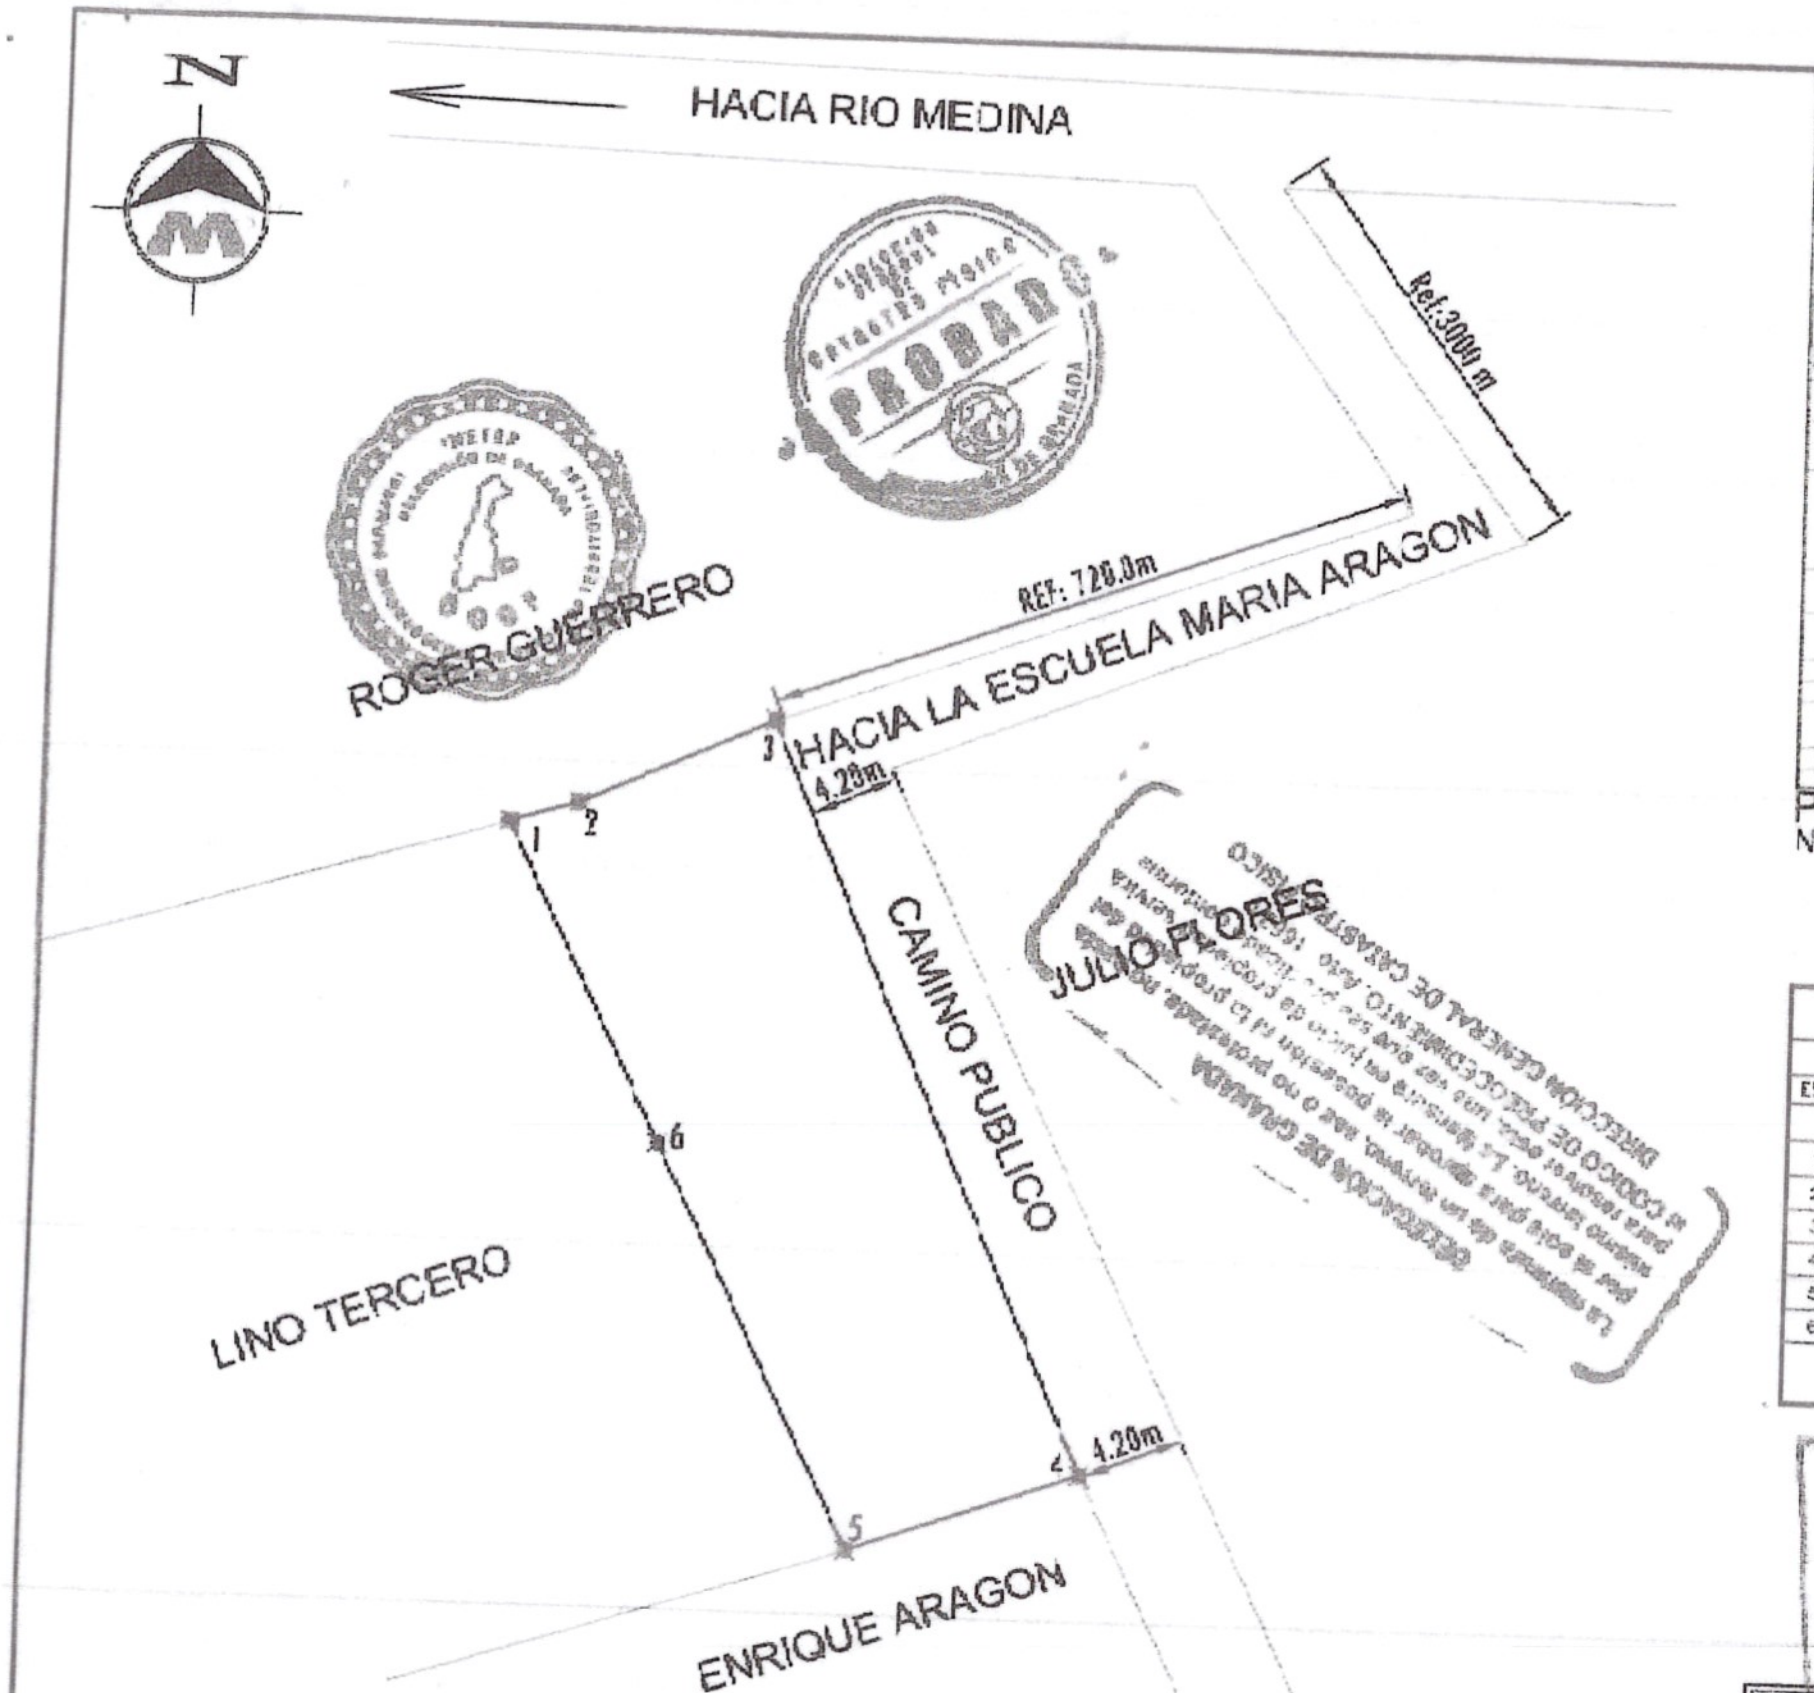

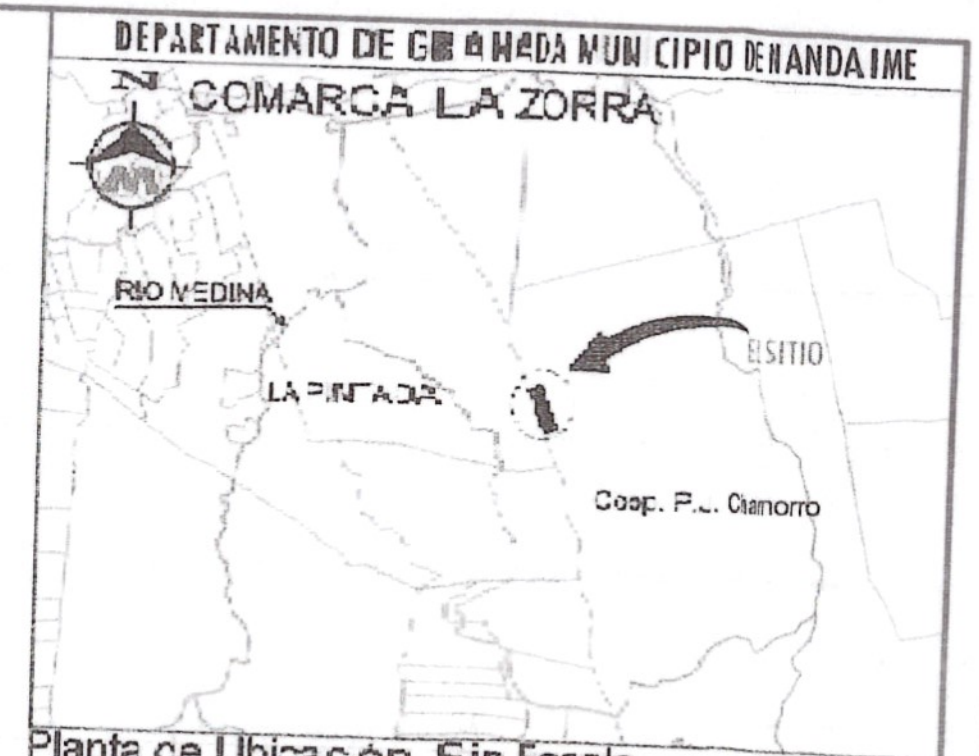

Planta de Ubicación Sin Escala
Número Catastral: 2951-2-15-000-02056

COORDENADAS NO VINCULADAS A LA RED GEODESICA NICARAGUA

CUADRO DE CONSTRUCCION

ADC EST	ADC PV	RUMBO	DISTANCIA	V	COORDENADAS Y	COORDENADAS X
				1	1,232,793.814	599,344.9397
1	2	N 75°42'21.44" E	38.24	2	1,232,803.986	599,379.7415
2	3	N 62°45'41.82" E	10.[illegible]	3	1,232,8[illegible].959	599,477.4101
3	4	S 23°46'32.26" E	40.[illegible]	4	1,232,477.2711	599,640.9743
4	5	S 70°46'32.68" W	16.5	5	1,232,456.743	599,524.7159
5	6	N 25°40'03.27" W	22.5	6	1,232,636.115	599,424.6763
6	1	N 22°47'31.19" W	10.[illegible]	1	1,232,793.814	599,344.9397

SUPERFICIE = 53,066.66 m2

MORGAN
Servicios Topográficos
Ing. Bosco Javier Morgan
Lic. Catastral EMM100426
Cel: 8883 7368

Karen Gissel Vélez Cruz cedula 202-070696-0002X
Actúa en representación de menor Matías Adrián García Vélez

Objeto Lev: Venta Total de Bien Inmueble	Número Catastral: 2951-2-15-000-02056	Fecha 29 de Octubre del 2025 FIRMA:
Enajenante: Víctor Manuel Cruz Alvarado Cédula: 202-120668-0001K	Ubicación: Comarca La Zorra Nandaime, Cooperativa Pedro Joaquín Chamorro, Municipio de Nandaime. Departamento de Granada.	Ejecuta Ing. Bosco Javier Morgan Lic. Catastral EMM100426 Cel: 8883 7368 Email: ingmorgan1968@gmail.com www.morgancontrucciones.com
Adquiriente: Matías Adrián García Vélez Partida de Nacimiento Tomo:10023 Folio 214 Partida: 214	Área: 53,066.66m2 = 75,273.38 vrs2= 7.53Mnz	Escala: 1 / 5,000

Transacción	Cudoc	Objeto Plano	Área (m²)	No. Lote
T-46G4UC-001	0039912	TRASPASO TOTAL	53,153.05	
Parcela Objeto	52999246937823		Documento	WBBYSN7
No. Licencia: BMM100426	Fecha Aprobación: 4/11/2025		Fecha Vencimiento: 4/11/2026 10:13:12	