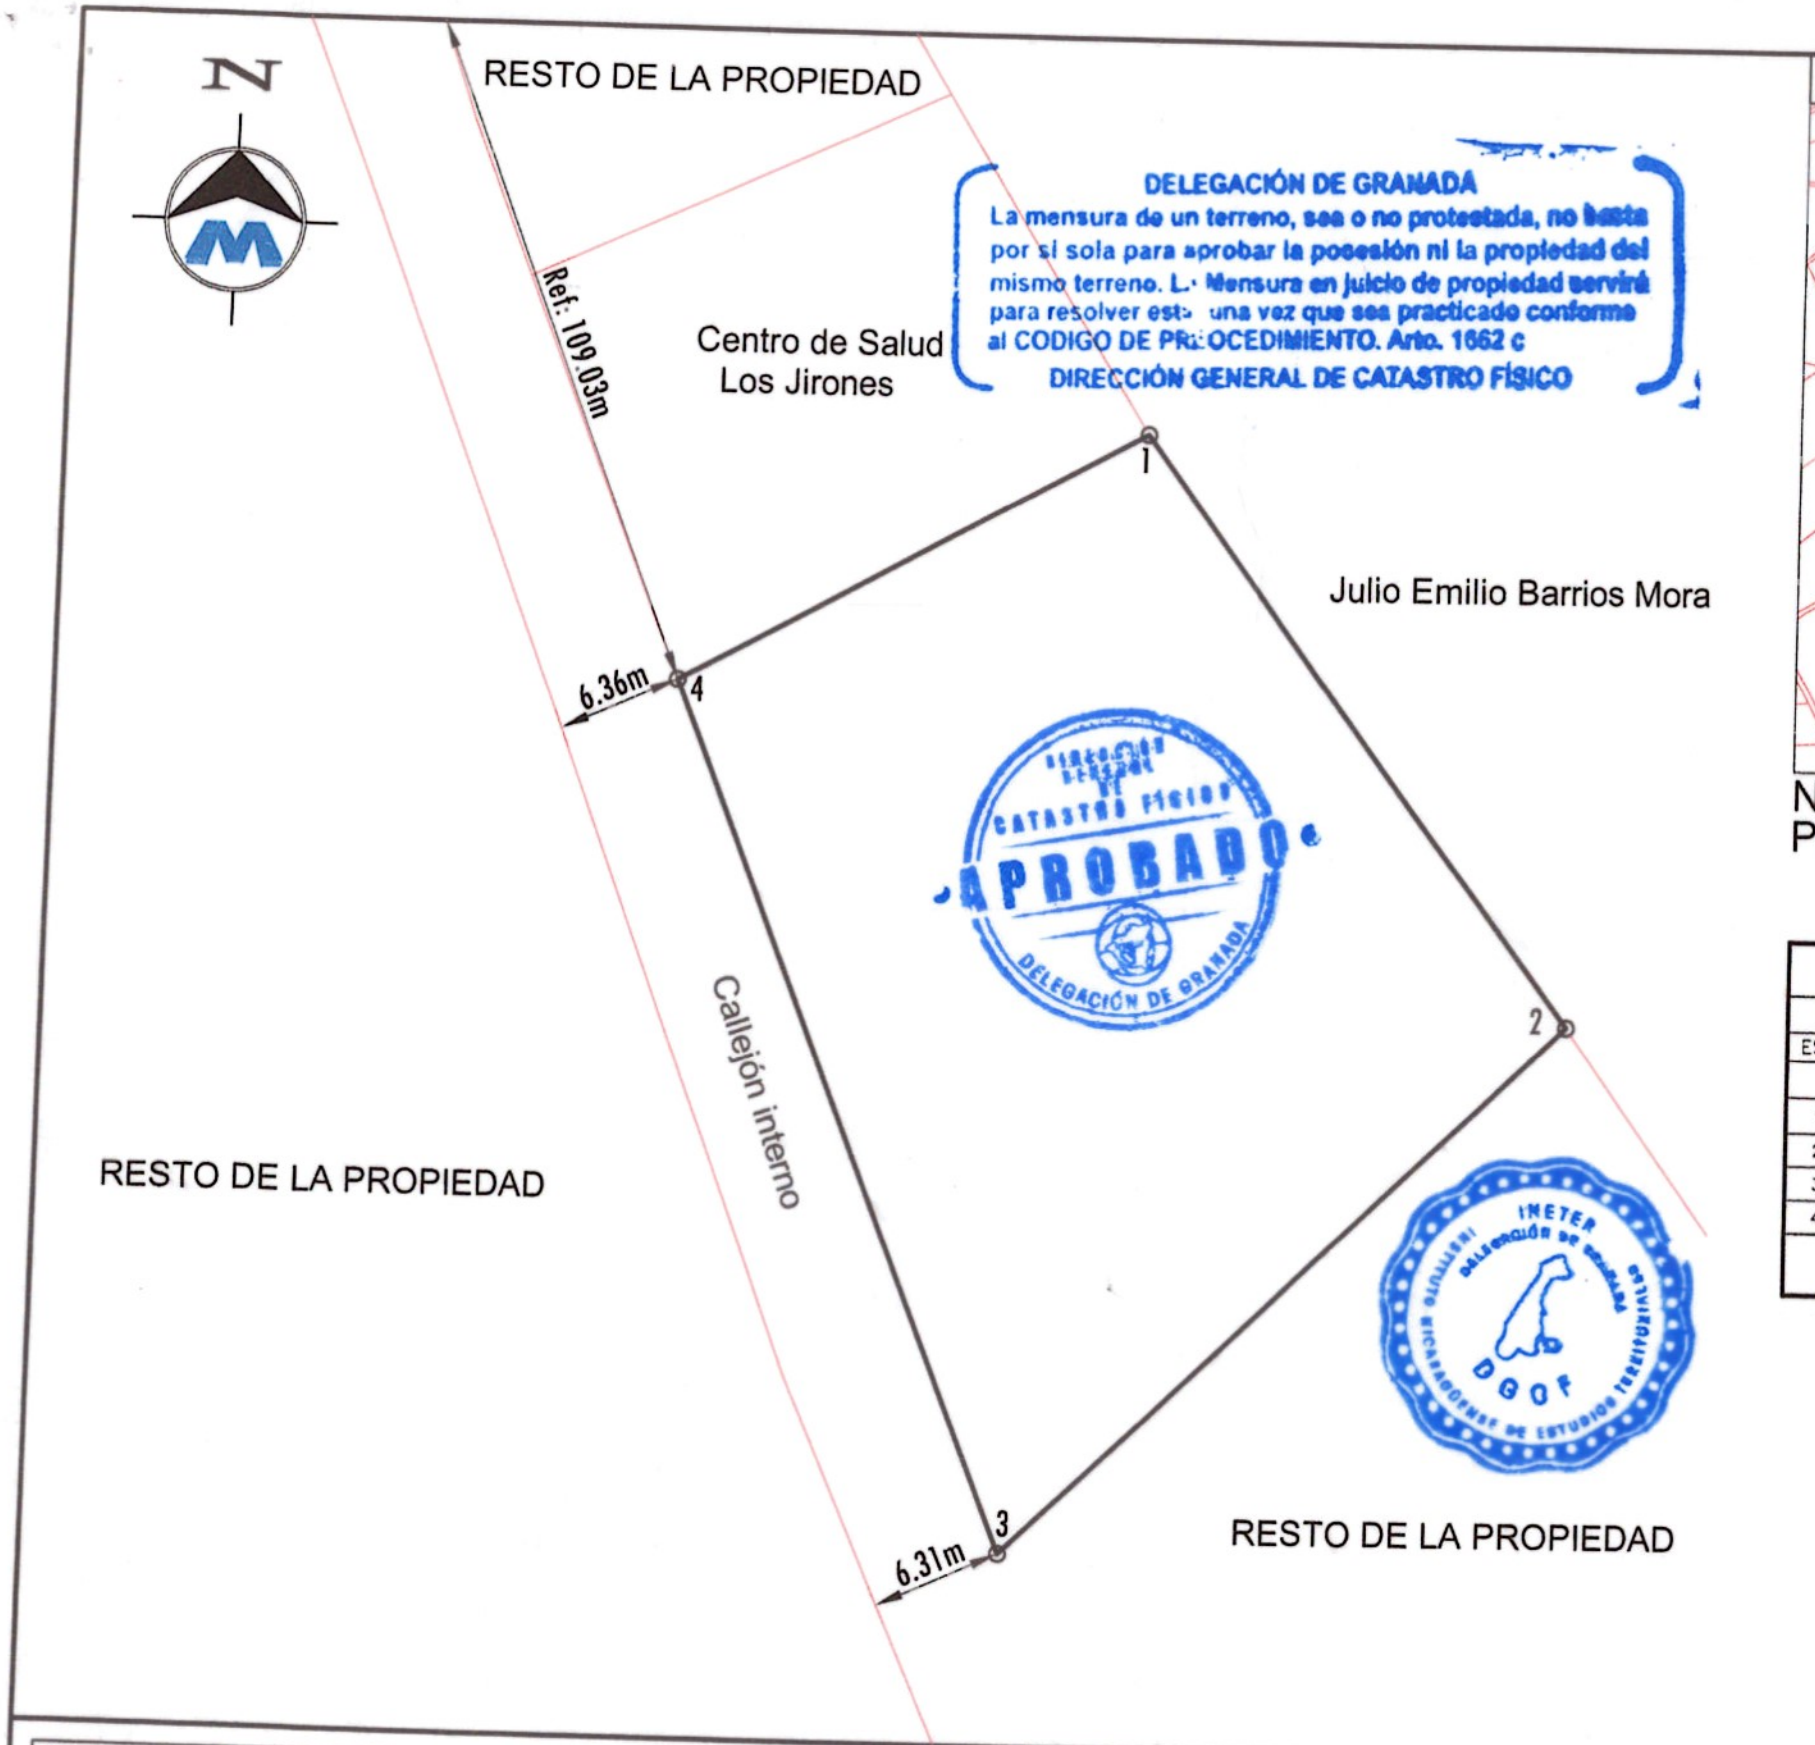

DELEGACIÓN DE GRANADA
La mensura de un terreno, sea o no protestada, no basta por sí sola para aprobar la posesión ni la propiedad del mismo terreno. La Mensura en juicio de propiedad servirá para resolver esta una vez que sea practicado conforme al CODIGO DE PROCEDIMIENTO. Arto. 1662 c
DIRECCIÓN GENERAL DE CATASTRO FÍSICO

DIRECCIÓN GENERAL DE CATASTRO FÍSICO APROBADO DELEGACIÓN DE GRANADA

INETER DELEGACIÓN DE GRANADA DGOF

DEPARTAMENTO DE GRANADA MUNICIPIO DE DIRIA

Número Catastral: 2951-1-15-000- 53200
Planta de Ubicación Sin Escala

COORDENADAS NO VINCULADAS A LA RED GEODESICA DE NICARAGUA

CUADRO DE CONSTRUCCION

LADO EST	LADO PV	RUMBO	DISTANCIA	V	COORDENADAS Y	COORDENADAS X
				1	1,310,502.2670	600,637.8080
1	2	S 36°54'14.40" E	36.390	2	1,310,473.1681	600,659.6592
2	3	S 46°06'28.85" W	38.627	3	1,310,446.3878	600,631.8225
3	4	N 22°00'36.26" W	46.494	4	1,310,489.4933	600,614.3979
4	1	N 61°22'51.42" E	26.668	1	1,310,502.2670	600,637.8080

SUPERFICIE = 1,313.44Om2 = 1,863.00Vrs2

MORGAN CONSTRUCCIONES
Ing. Bosco Javier Morgan
Lic. MTI 5365
Tel: 8883-7568

Objeto Lev: Venta Parcial (Desmembración)	Número Catastral: 2951-1-15-000- 53200		FIRMA:	SELLO
Enajenante: Ricardo Moya Jaenz Ced: 204-200562-0002P c.c. Ricardo Jose Moya Jaenz.	Ubicación: Cmca. Los Jirones, costado Sur del Centro de salud. Municipio de Diria, Departamento de Granada.		Ejecuta: Ing.Bosco Javier Morgan Lic. Catastral: BMM100426 Cel: 8883-7568 Email: ingmorgan73@gmail.com servicios topograficos	
Adquiriente: Scarleth Robleto Gomez Ced: 201-090265-0003D	Área: 1,313.44 m² = 1,863.00Vrs²	Escala: 1 / 500	Fecha: 09 de Octubre 2025	

Transacción	Cudoc	Objeto Plano	No. Lote
T-46FA6T-001	0039124	DESMEMBRACIÓN	
Parcela Objeto	63010064044212	Área (m²)	
		1,313.44	
No. Licencia: BMM100426	Fecha Aprobación: 25/10/2025	Documento	Fecha Vencimiento: 25/10/2026
		W8BYP2F	

Objeto Lev: Venta Parcial (Desmembración)
Número Catastral: 2951-1-15-000- 53200

COORDENADAS NO VINCULADAS A LA RED GEODESICA DE NICARAGUA

CUADRO DE CONSTRUCCION

LADO		RUMBO	DISTANCIA	V	COORDENADAS	
EST	PV				Y	X
				1	1,310,502.2670	600,637.8080
1	2	S 36°54'14.40" E	36.390	2	1,310,473.1681	600,659.6592
2	3	S 46°06'28.85" W	38.627	3	1,310,446.3878	600,631.8225
3	4	N 22°00'36.26" W	46.494	4	1,310,489.4933	600,614.3979
4	1	N 61°22'51.42" E	26.668	1	1,310,502.2670	600,637.8080

SUPERFICIE = 1,313.440m2 = 1,863.00Vrs2

MORGAN CONSTRUCCIONES
Ing. Bosco Javier Morgan
Lic. MTI 5365
Tele: 88837568

Ejecuta: Ing. Bosco Javier Morgan
Lic. Catastral: BMM100426
Cel: 8883-7568 Email: ingmorgan73@gmail.com
servicios topograficos