Transacción	Cudoc	Objeto Plano	Area (m²)	No. Lote
T-46EKOJ-001	0038636	VERIFICACIÓN	31,725.55	
Parcela Objeto	6209602827851B		Documento	W8BZV5W
No. Licencia: BMN100426	Fecha Aprobación: 10/11/2025		Fecha Vencimiento: 10/11/2025	

La mensura de un terreno, sea o no protocolada, no basta por sí sola para acreditar la posesión o la propiedad del mismo terreno. La Mensura en juicio de propiedad cerrada, para resolver esta una vez que sea practicado conforme el CODIGO DE PROCEDIMIENTO. Arts. 1462c
DIRECCIÓN GENERAL DE CATASTRO FÍSICO

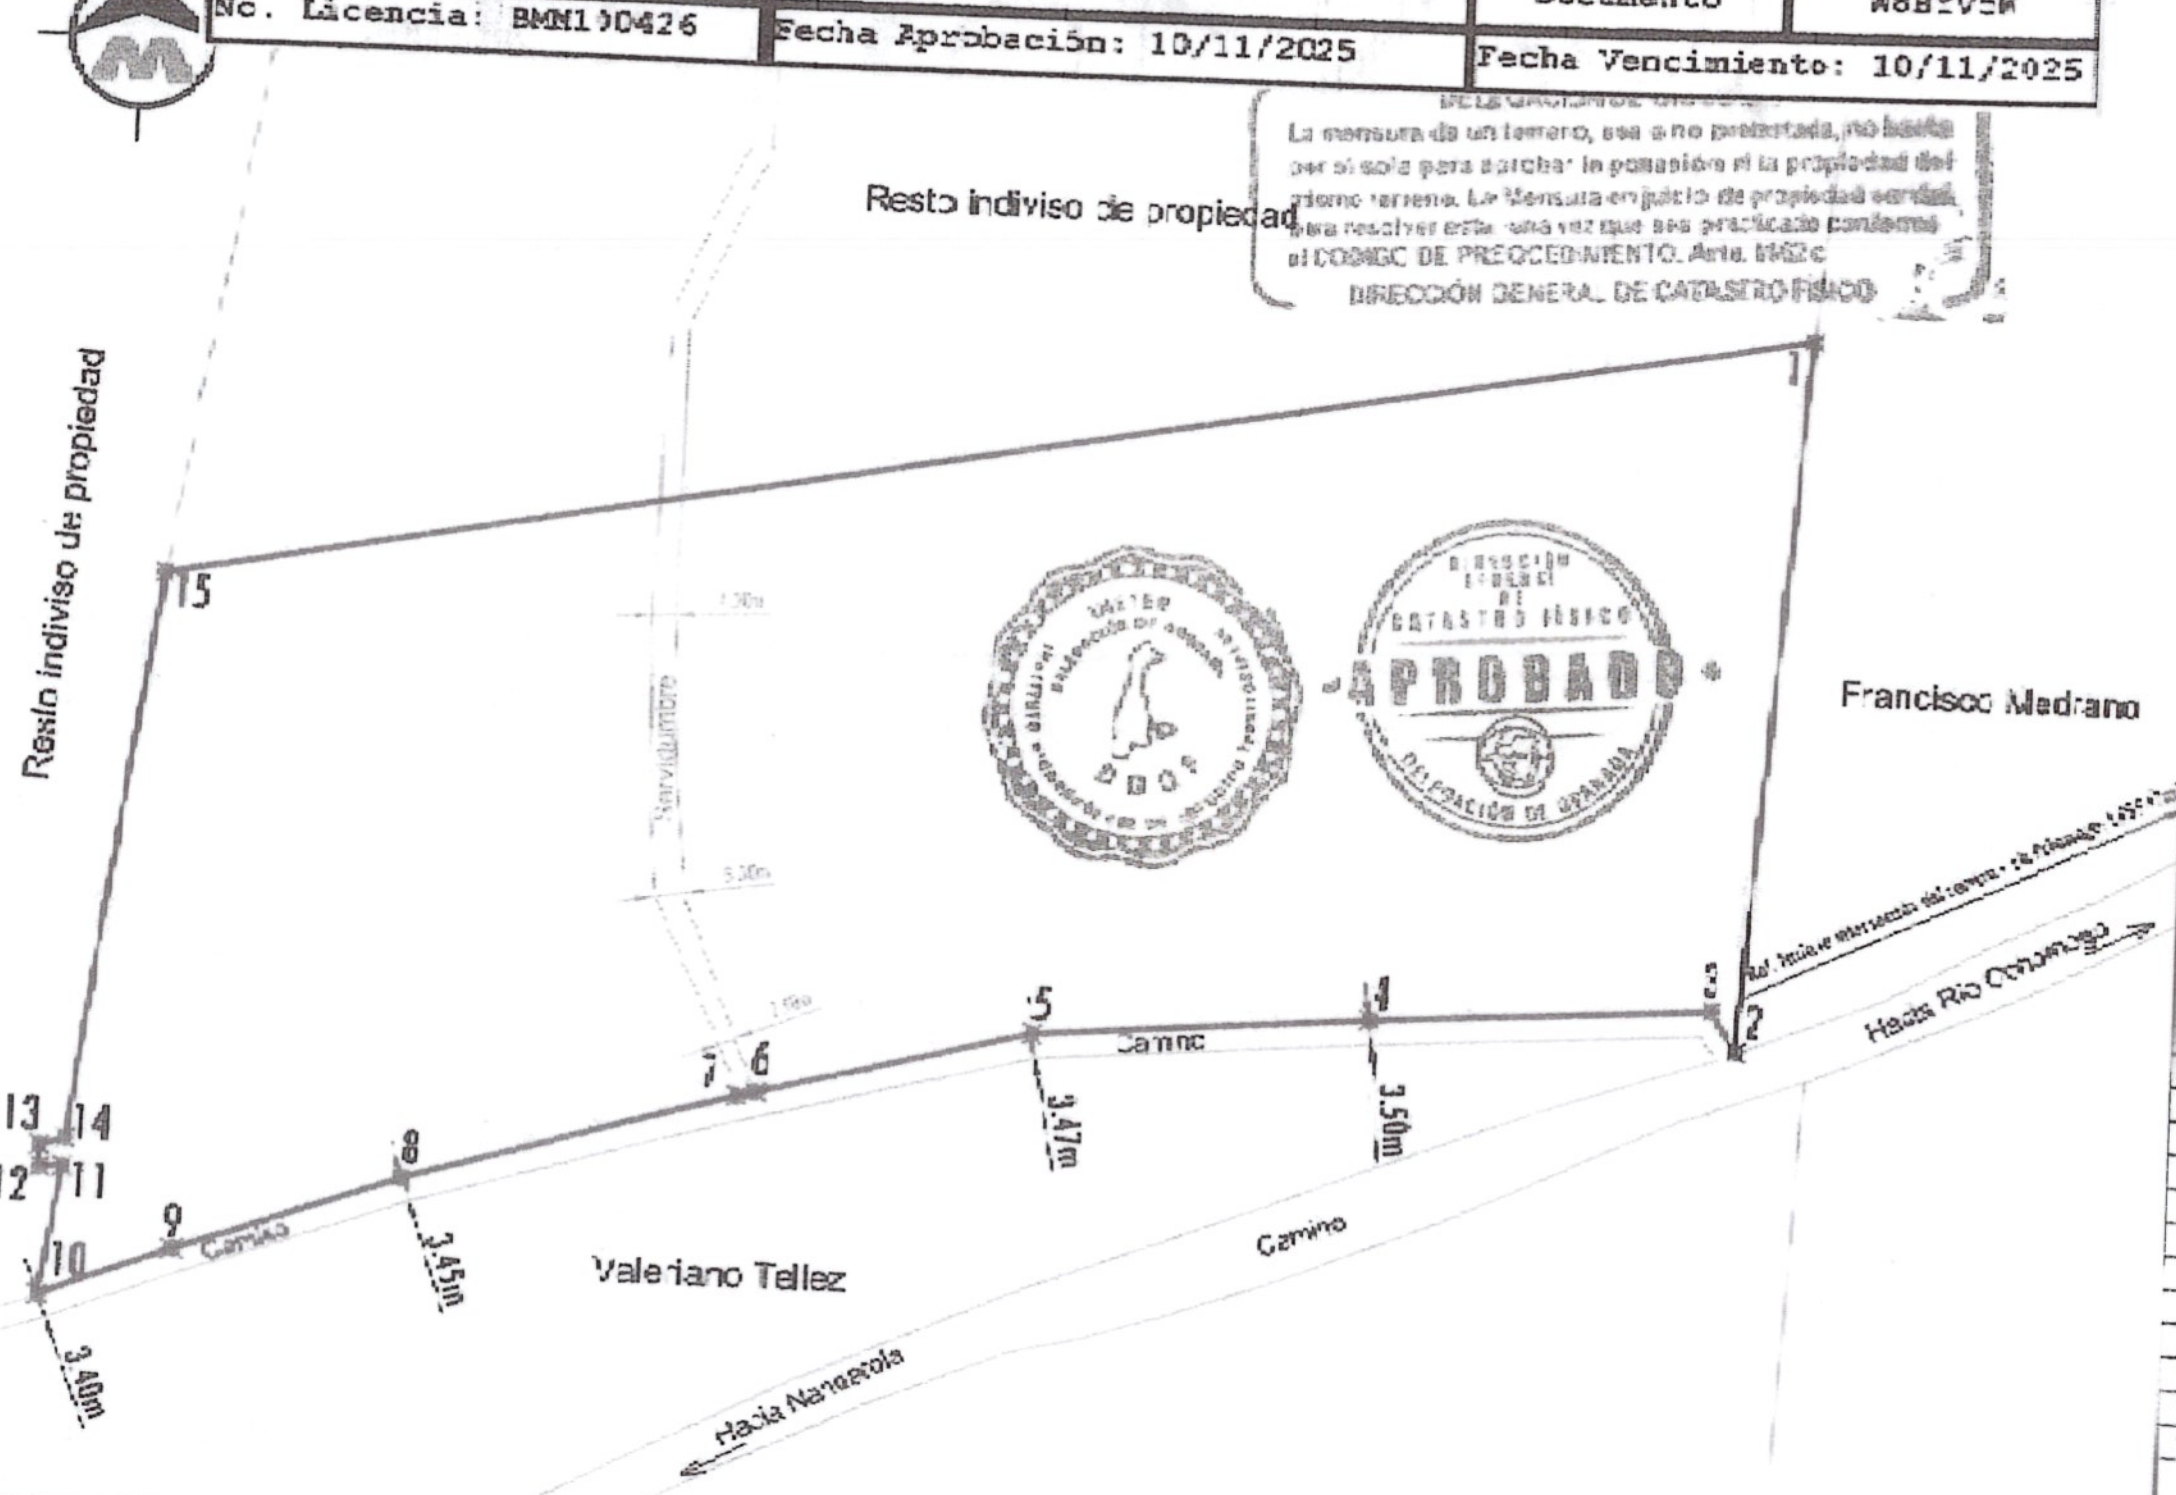

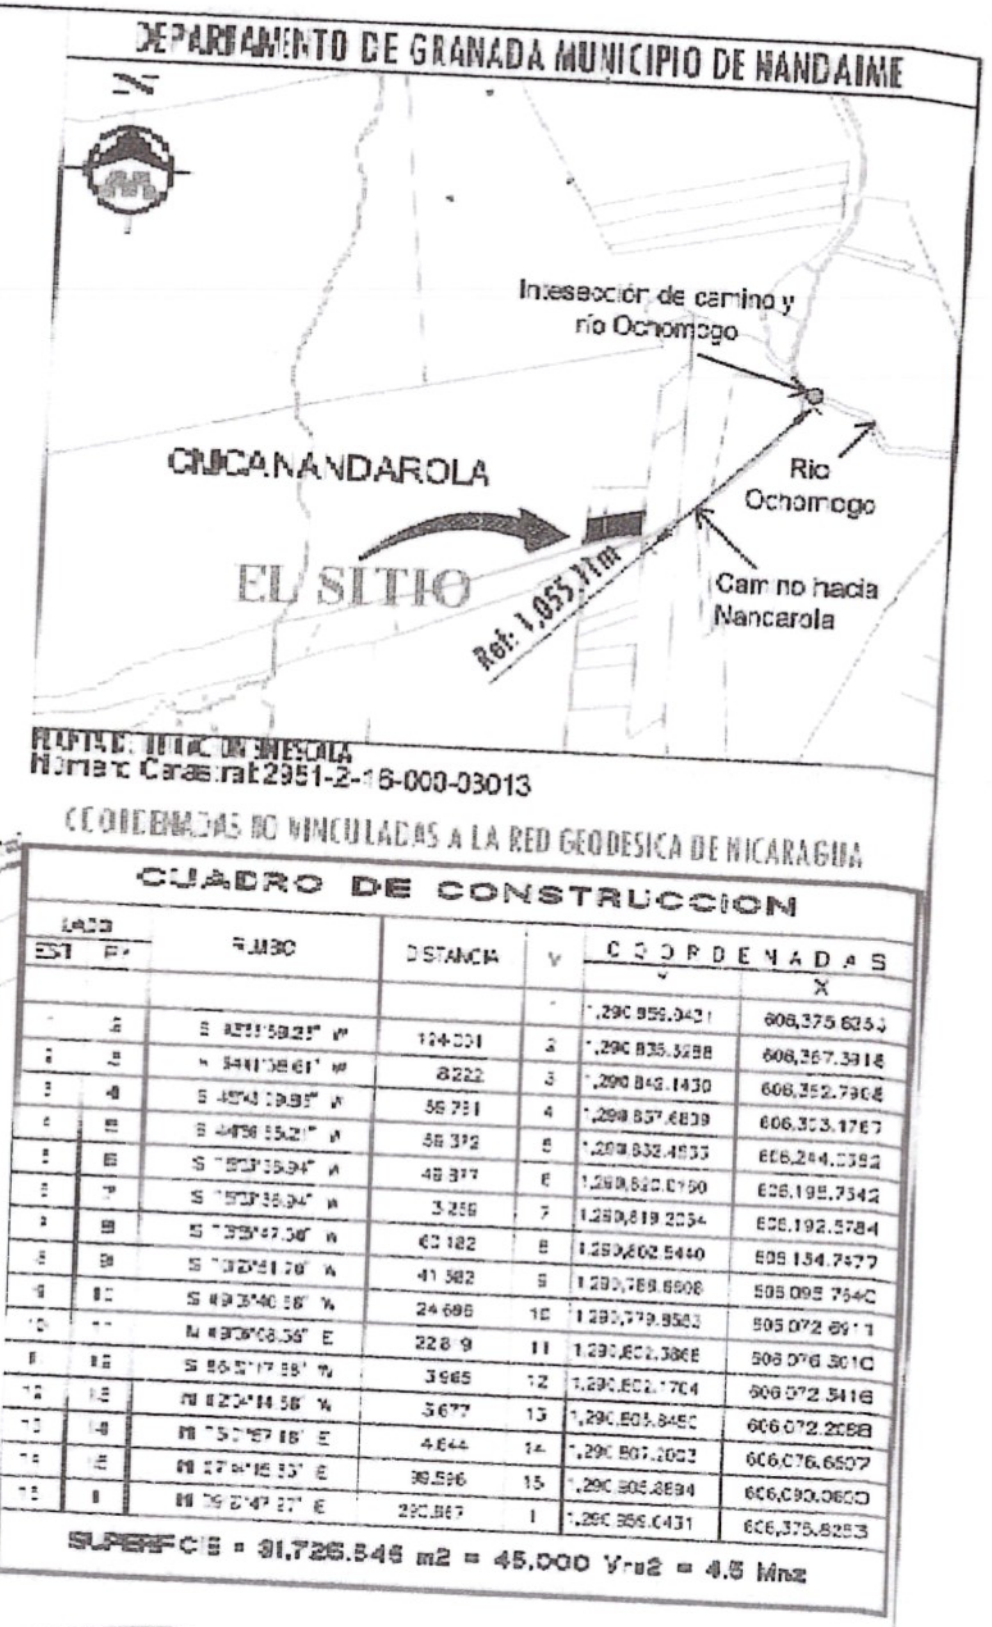

CUADRO DE CONSTRUCCION

LADO EST	PV	RUMBO	DISTANCIA	V	COORDENADAS Y	COORDENADAS X
					1,290,955.0431	606,375.6253
1	2	S 85°15'59.21" W	104.031	2	1,290,835.5288	606,367.3916
2	3	N 84°13'58.61" W	8.222	3	1,290,843.1430	606,352.7908
3	4	S 45°43'29.95" W	56.731	4	1,290,837.6839	606,303.1767
4	5	S 44°56'55.21" W	56.372	5	1,290,832.4533	606,254.0382
5	6	S 75°53'35.94" W	48.377	6	1,290,820.0150	606,198.7542
6	7	S 75°53'35.94" W	3.259	7	1,290,819.2234	606,192.5784
7	8	S 75°35'47.36" W	63.182	8	1,290,802.5440	606,134.7477
8	9	S 73°25'51.28" W	41.382	9	1,290,788.6908	606,095.7540
9	10	S 49°34'40.56" W	24.686	10	1,290,779.9583	606,072.6911
10	11	N 49°06'08.56" E	228.9	11	1,290,851.3868	606,076.3010
11	12	S 86°51'17.55" W	3.965	12	1,290,851.1704	606,072.3416
12	13	N 82°04'14.56" W	3.677	13	1,290,850.8450	606,072.2088
13	14	N 75°51'57.18" E	4.644	14	1,290,851.2002	606,076.6507
14	15	N 27°44'16.33" E	39.596	15	1,290,905.8894	606,090.0600
15	1	N 79°24'47.27" E	290.867	1	1,290,955.0431	606,375.6253

SUPERFICIE = 31,725.546 m2 = 45,000 Vrs2 = 4.5 Mnz

El objeto de este plano es para dar inicio proceso de Declaratoria de Herederos

Objeto: Lev. Verificación de Área de su parte indivisa Propietario: Julia Virginia Ticay Peña Certificado de defunción Tomo: 10005 Folio: 228 Partida: 228	Número Catastral: 2951-2-16-000-03013	FIRMA:
Solicitante: Denis Humberto Ruiz Ticay Cédula: 202-050978-0002_	Ubicación: Comarca Nancarola De la Intersección del camino y río Ochomogo 1,055.11 m² al Suroeste Municipio de Nandaime, Departamento de Granada	Ejecuta: Ing. Bosco Javier Morgan Lic. Catastral: BMN-100426 Cel: 8883-7568 SERVICIOS TOPOGRAFICOS
	Área: 31,725.545 m² = 45,000.00 Vrs² = 4.5 Mnz — Escala: 1/1,750	Fecha: 19 de Septiembre del 2025

MORGAN
Servicios Topograficos
Ing. Bosco Javier Morgan
Lic. Catastral: BMN-100426
Cel: 8883 7568