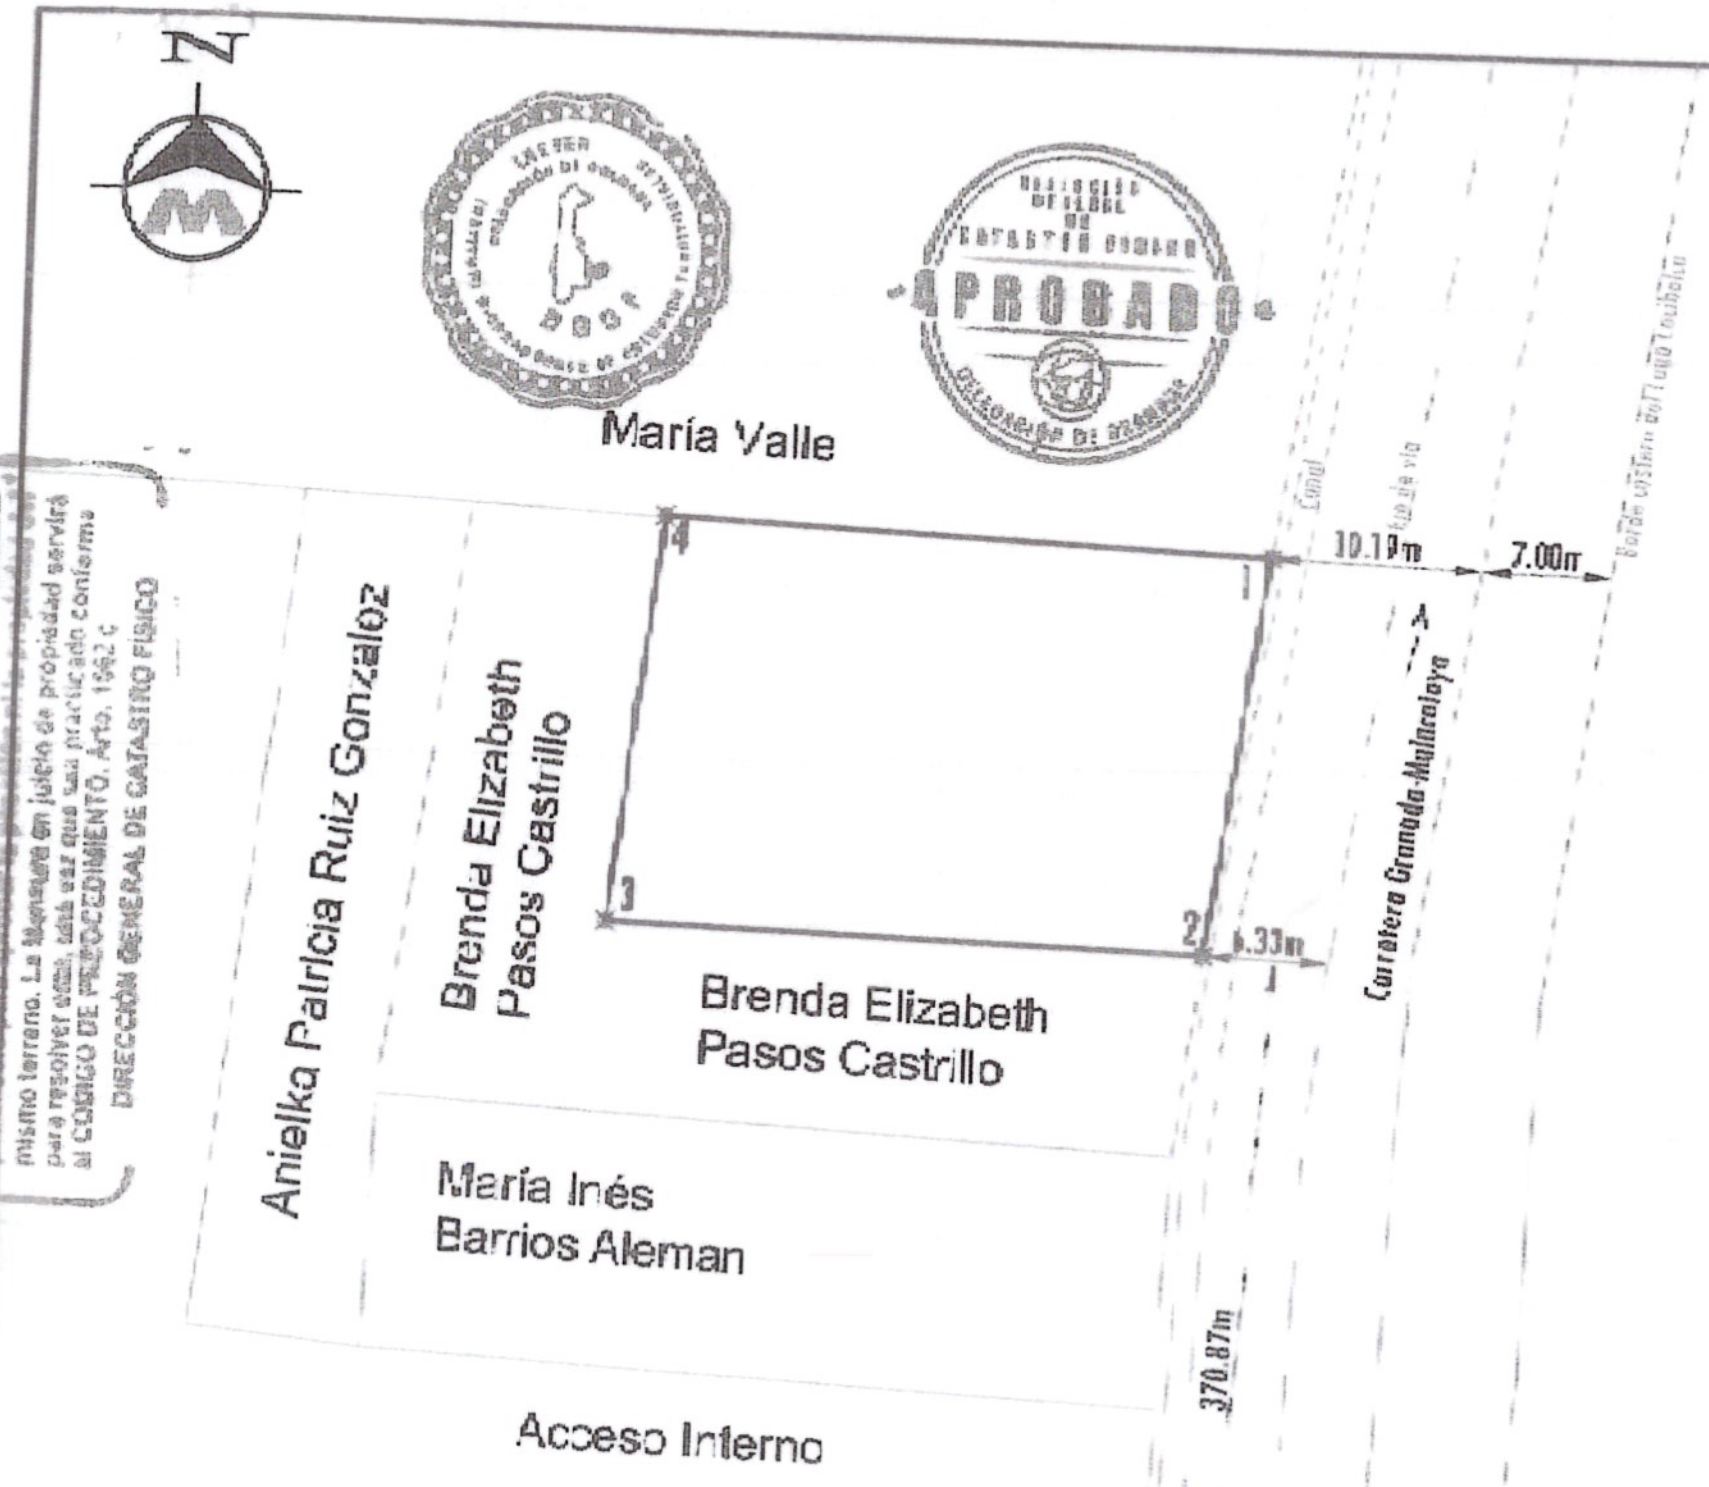

DELEGACIÓN DE GRANADA
La menura de un terreno, sea o no protestada, no garantiza
mismo terreno. La Mensura en juicio de propiedad servirá
para resolver esta vez que sea practicado conforme
el CÓDIGO DE PROCEDIMIENTO. Arto. 1962 C
DIRECCIÓN GENERAL DE CATASTRO FÍSICO

DEPARTAMENTO DE GRANADA MUNICIPIO DE GRANADA

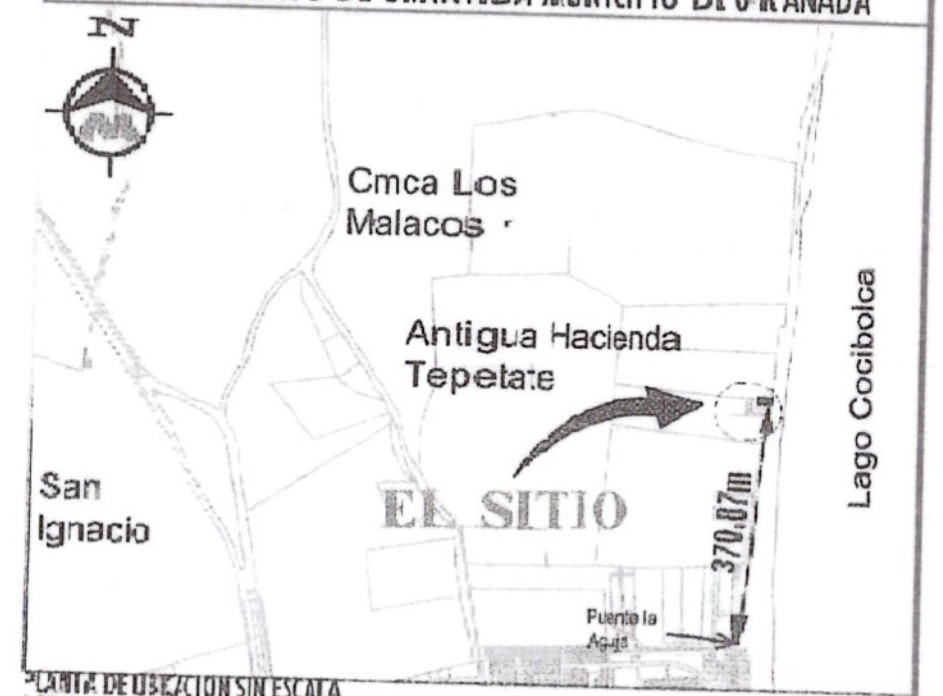

PLANTA DE UBICACION SIN ESCALA
Número Catastral: 3051-4-05-000

COORDENADAS NO VINCULADAS A LA RED GEODESICA DE NICARAGUA

CUADRO DE CONSTRUCCION

LADO ESTACION	LADO PUNTO	RUMBO	DISTANCIA	V	COORDENADAS Y	COORDENADAS X
				1	1,321,813.9600	514,810.7400
1	2	S 03°53'24.45" W	20.046	2	1,321,793.9600	514,809.3800
2	3	S 88°07'48.90" W	30.036	3	1,321,792.9200	514,779.3600
3	4	N 03°32'38.41" E	19.898	4	1,321,812.7800	514,780.5900
4		N 87°52'21.28" E	30.17	1	1,321,813.9600	514,810.7400

SUPERFICIE = 598.234 m2 = 848.54 Vrs2

MORGAN
Servicios Topograficos
Ing Bosco Javier Morgan
Lic Catastral BMM100426
Cel 8883-7569

Objeto Lev: Venta Total	Número Catastral: 3051-4-05-000	FIRMA:
Enajenante: Roberto Carlos Pavon Tercero Cédula: 201-051179-0009J	Ubicación: Del Puente La Aguja 370.87 m al Norte, Carretera Granada-Malacatoya Municipio de Granada, Departamento de Granada.	Ejecuta: Ing.Bosco Javier Morgan Lic. Catastral: BMM100426 Celular: 8883-7569 SERVICIOS TOPOGRAFICOS
Adquiriente: Karla Vanessa Gomez Maycrga Cédula: 201-190473-1000D	Área 598.234 m² = 848.54 Vrs² — Escala: 1:500	Fecha: 18 de Septiembre del 2025

Transacción	Cudoc	Objeto Plano	Área (m²)	No. Lote
T-46ERS4-001	0038791	TRASPASO TOTAL	598.23	
Parcela Objeto	6312417787171 0		Documento	
No. Licencia: BMM100426	Fecha Aprobación: 10/11/2025		W8BYVHI	Fecha Vencimiento: 10/11/2026 10:11:14