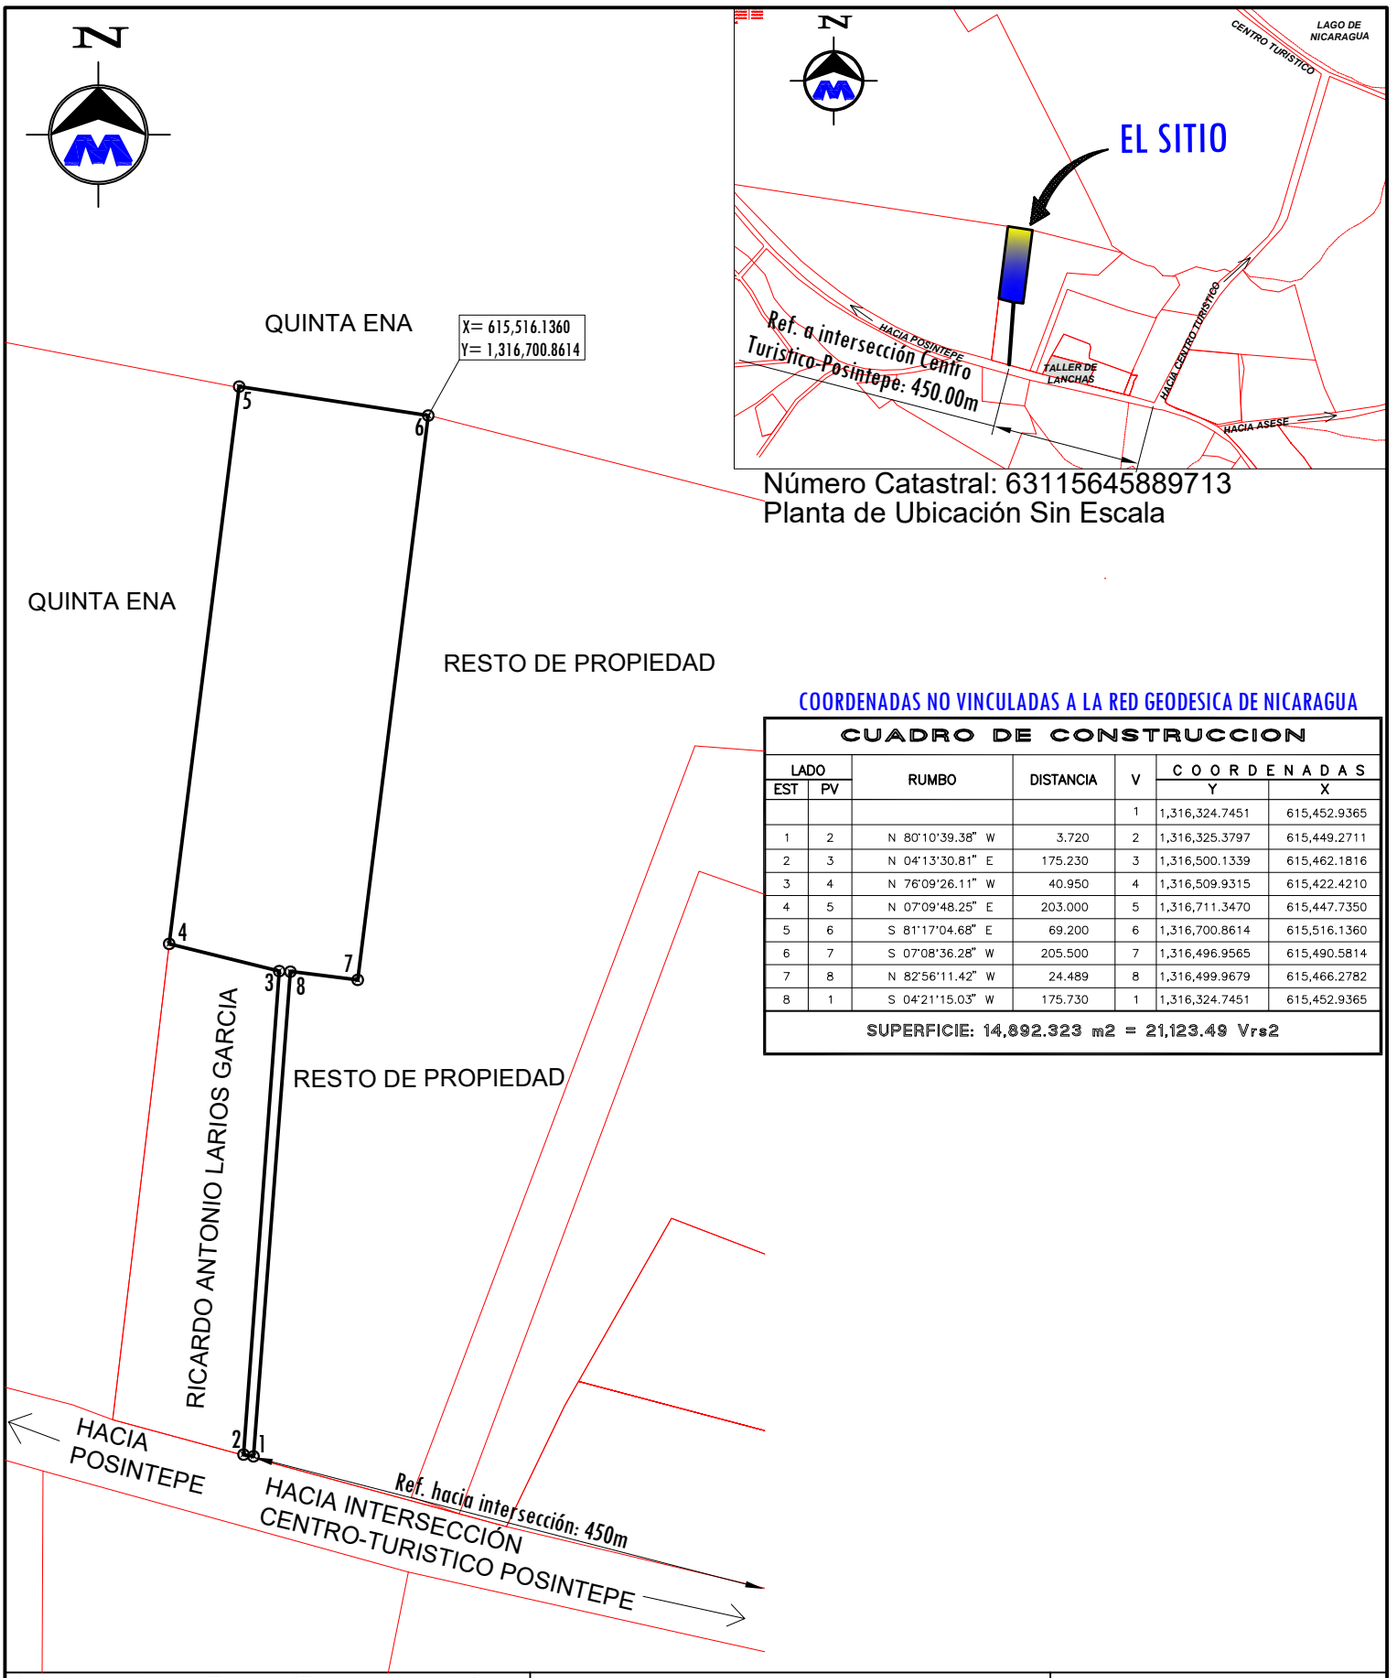

Número Catastral: 63115645889713
Planta de Ubicación Sin Escala

COORDENADAS NO VINCULADAS A LA RED GEODESICA DE NICARAGUA

CUADRO DE CONSTRUCCION

LADO EST	LADO PV	RUMBO	DISTANCIA	V	COORDENADAS Y	COORDENADAS X
				1	1,316,324.7451	615,452.9365
1	2	N 80°10'39.38" W	3.720	2	1,316,325.3797	615,449.2711
2	3	N 04°13'30.81" E	175.230	3	1,316,500.1339	615,462.1816
3	4	N 76°09'26.11" W	40.950	4	1,316,509.9315	615,422.4210
4	5	N 07°09'48.25" E	203.000	5	1,316,711.3470	615,447.7350
5	6	S 81°17'04.68" E	69.200	6	1,316,700.8614	615,516.1360
6	7	S 07°08'36.28" W	205.500	7	1,316,496.9565	615,490.5814
7	8	N 82°56'11.42" W	24.489	8	1,316,499.9679	615,466.2782
8	1	S 04°21'15.03" W	175.730	1	1,316,324.7451	615,452.9365

SUPERFICIE: 14,892.323 m2 = 21,123.49 Vrs2

Objeto Lev: Venta Parcial (Desmembración)	Número Catastral: 63115645889713	FIRMA:
Enajenante: Johana Patricia Jaime Cruz Ced:202-281283-0000B Virginia Patricia Cruz Martinez Ced:202-281283-0000B	Ubicación: Carretera Posintepe ASESE, de la intersección carretera del Centro Turistico-Posintepe 450m al Oeste. Municipio de Granada, Departamento de Granada.	Ejecuta: Ing.Bosco Javier Morgan Lic. Catastral: BMM100426 Cel: 8883-7568 Email: ingmorgan73@gmail.com servicios topograficos
Adquiriente: Darling Stick Ortega Aragon Ced: 201-180293-0006Y	Área:14,892.32m²=21,123.49Vrs² Escala:1 / 500	Fecha: 03 de Junio 2025

ESPACIO PARA ESQUELA