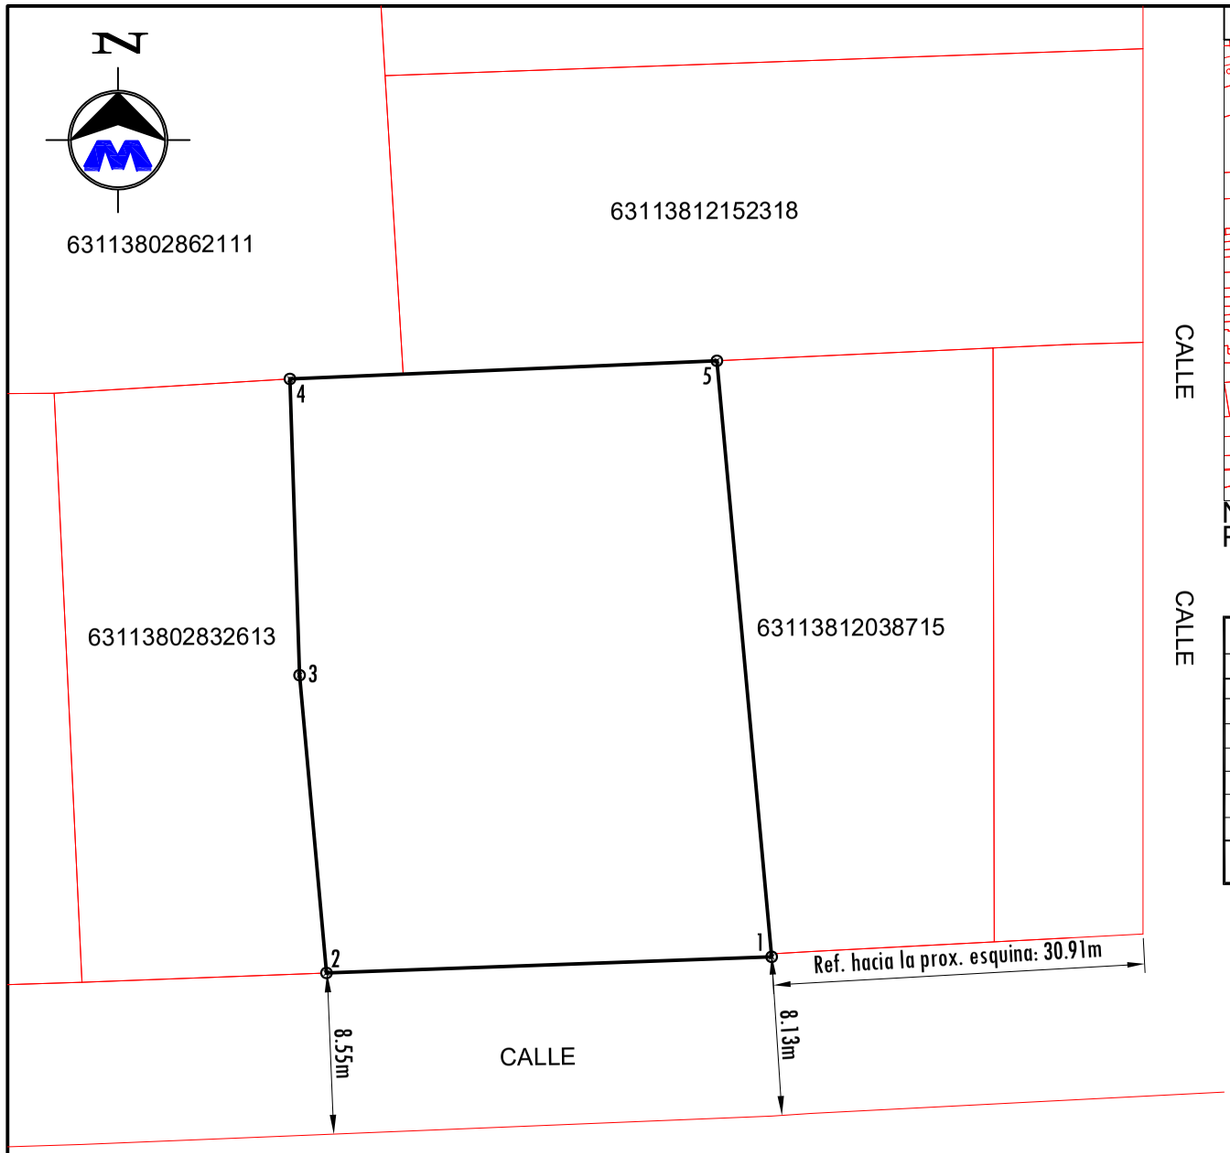

DEPARTAMENTO DE GRANADA MUNICIPIO DE GRANADA

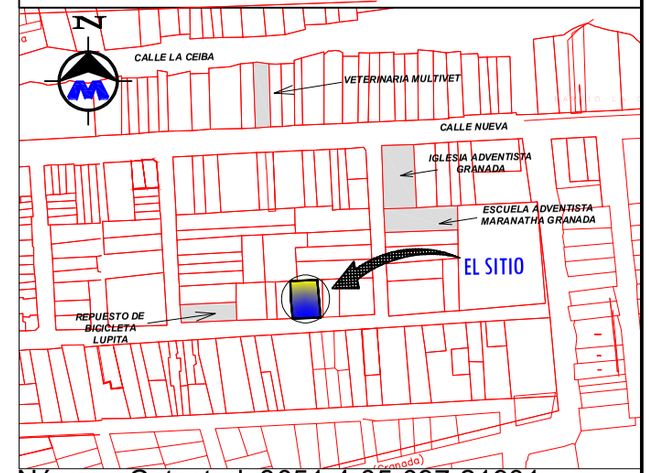

Número Catastral: 3051-4-05-097-21901
Planta de Ubicación Sin Escala

COORDENADAS NO VINCULADAS A LA RED GEODESICA DE NICARAGUA

CUADRO DE CONSTRUCCION

LADO EST	LADO PV	RUMBO	DISTANCIA	V	COORDENADAS Y	COORDENADAS X
				1	1,318,232.9990	613,109.8501
1	2	S 87°55'32.76" W	16.106	2	1,318,232.4160	613,093.7545
2	3	N 05°09'05.59" W	10.811	3	1,318,243.1829	613,092.7838
3	4	N 01°50'28.72" W	10.717	4	1,318,253.8947	613,092.4395
4	5	N 87°32'49.76" E	15.445	5	1,318,254.5557	613,107.8704
5	1	S 05°14'49.85" E	21.647	1	1,318,232.9990	613,109.8501

SUPERFICIE: 343.557 m2 = 487.30 Vrs2

ESPACIO PARA ESQUELA

Objeto Lev: Venta Total	Número Catastral: 3051-4-05-097-21901	FIRMA:
Enajenante: Dina Emerita Garcia Lara Ced.: 201-271048-0002L	Ubicación: De Iglesia Adventista Granada 1c al Sur, 30.91 m al O. Municipio de Granada, Departamento de Granada.	Ejecuta: Ing.Bosco Javier Morgan Lic. Catastral: BMM100426 Cel: 8883-7568 Email: ingmorgan73@gmail.com servicios topograficos
Adquiriente: Wilmer Ernesto Lacayo Carcache Ced.: 201-280386-0006Q	Área: 343.557 m² = 487.30 Vrs² — Escala: 1 / 250	Fecha: 22 de Marzo 2025