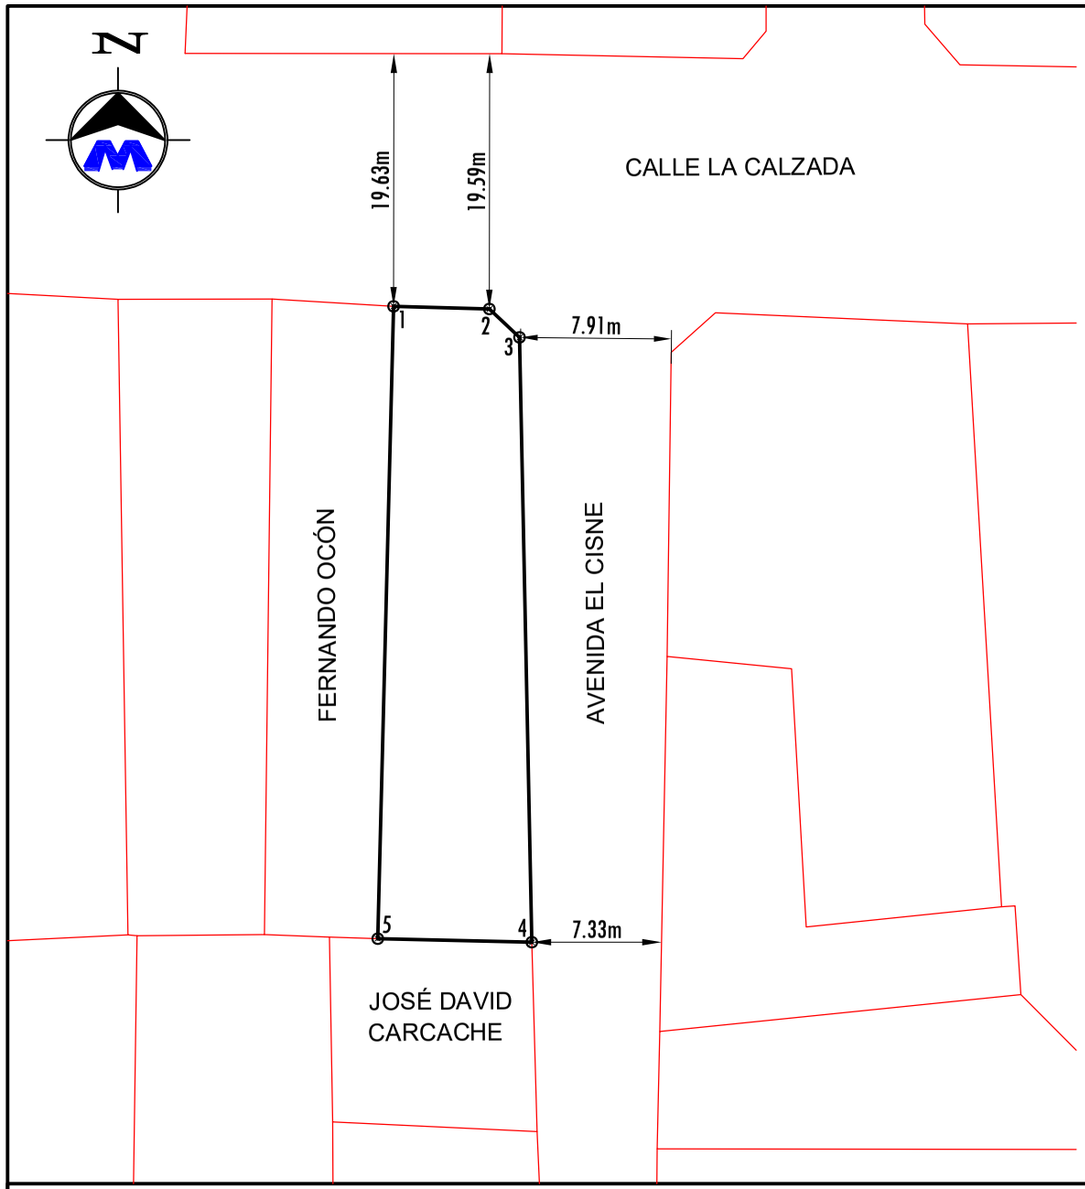

DEPARTAMENTO DE GRANADA MUNICIPIO DE GRANADA

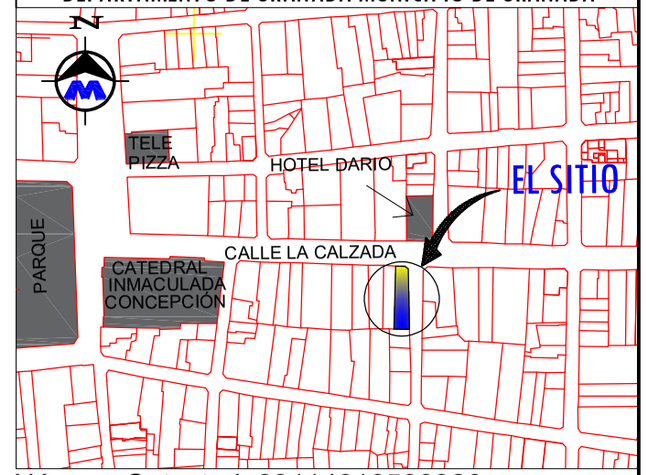

Número Catastral: 63114910509320
Planta de Ubicación Sin Escala

COORDENADAS NO VINCULADAS A LA RED GEODESICA DE NICARAGUA

CUADRO DE CONSTRUCCION

LADO EST	LADO PV	RUMBO	DISTANCIA	V	COORDENADAS Y	COORDENADAS X
				1	1,319,030.3530	614,163.9460
1	2	S 88°18'19.27" E	6.932	2	1,319,030.1480	614,170.8750
2	3	S 46°43'09.50" E	2.993	3	1,319,028.0960	614,173.0540
3	4	S 01°09'37.25" E	43.752	4	1,318,984.3530	614,173.9400
4	5	N 88°37'39.03" W	11.147	5	1,318,984.6200	614,162.7960
5	1	N 01°26'25.63" E	45.747	1	1,319,030.3530	614,163.9460

Área: 460.069 m² = 324.35 Vrs²

ESPACIO PARA ESQUELA

Objeto Lev: Transcripción por testameno abierto de su parte indivisa.	Número Catastral: 63114910509320	FIRMA:
Enajenante: Francisco Martin Monterrey Muñoz (Q.E.P.D.) Tomo: 108; Folio: 074; Partida: 074. Conocido registralmente como Martin Monterrey Muñoz	Ubicación: Esquina Noreste de Catedral Inmaculada Concepción de María, 1C al Este, M/D. Municipio de Granada, Departamento de Granada.	Ejecuta: Ing.Bosco Javier Morgan Lic. Catastral: BMM100426 Cel: 8883-7568 Email: ingmorgan73@gmail.com servicios topograficos
Adquiriente: Gladys de los Dolores Cuadra Sandino Ced: 201-150954-0007B. Conocida registralmente como Gladys Cuadra de Monterrey	Área: 460.069 m² = 324.35 Vrs² — Escala: 1 / 500	Fecha: 16 de Junio 2025