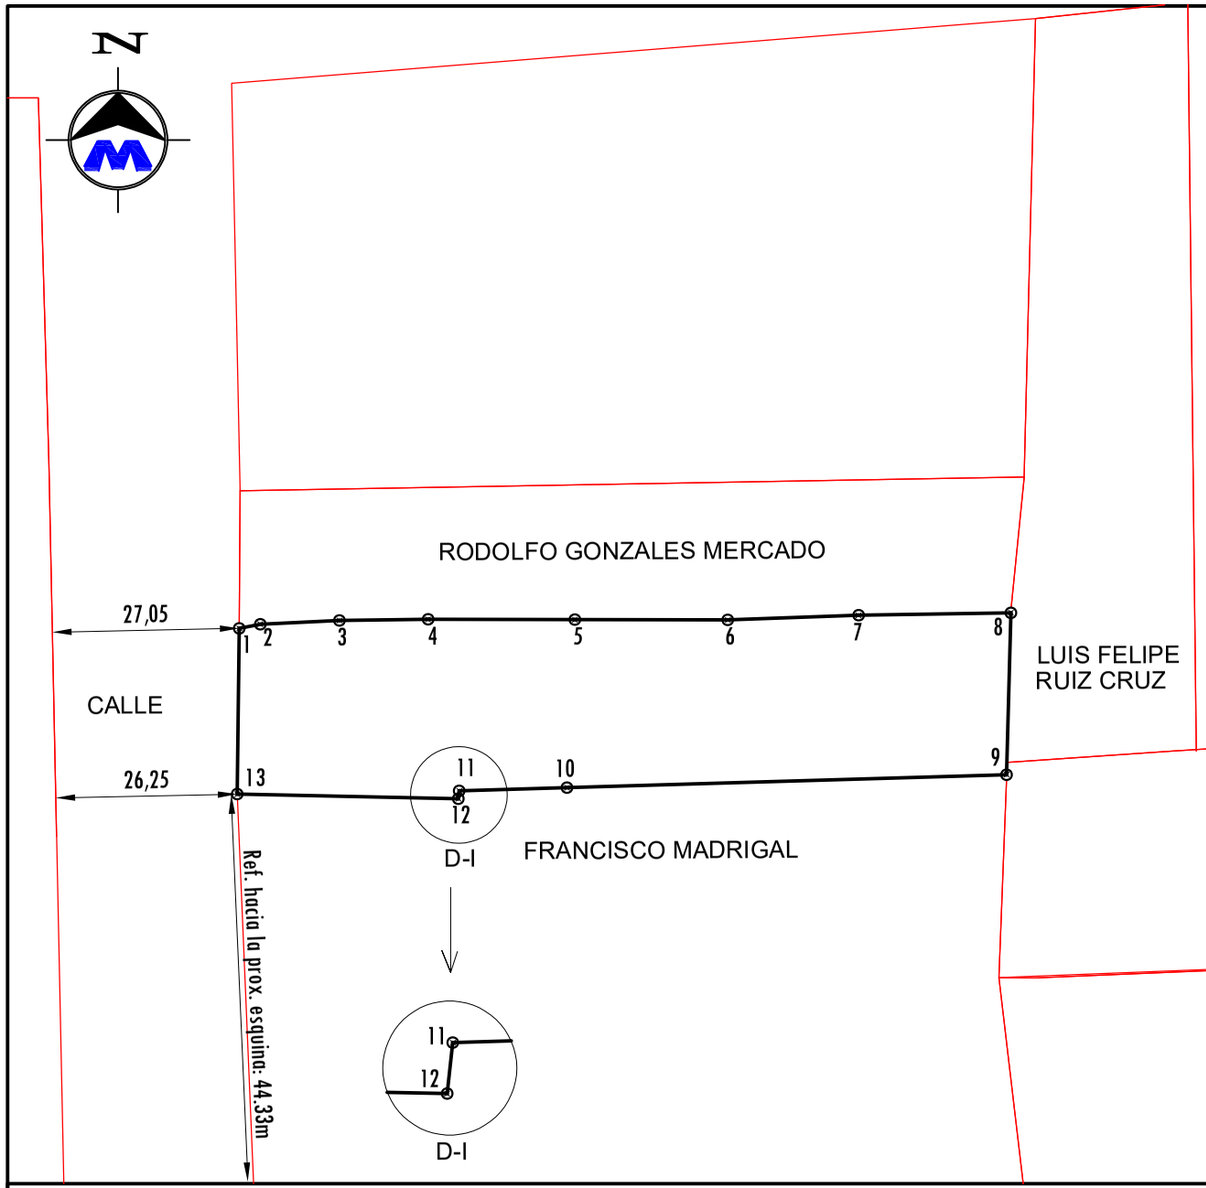

DEPARTAMENTO DE GRANADA MUNICIPIO DE GRANADA

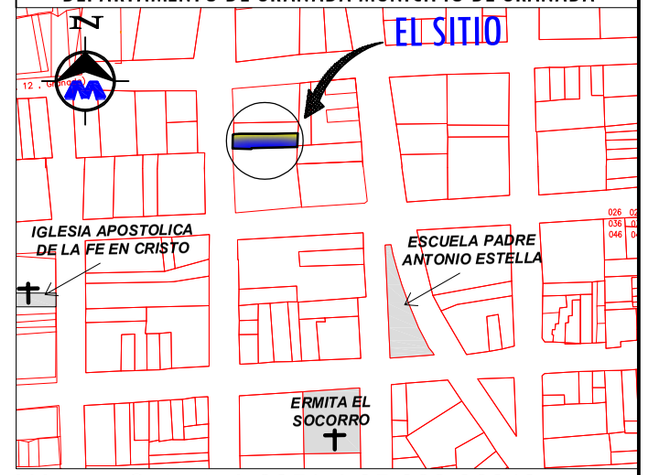

Número Catastral: 3051-4-05-036-06010
Planta de Ubicación Sin Escala

COORDENADAS NO VINCULADAS A LA RED GEODESICA DE NICARAGUA

CUADRO DE CONSTRUCCION

LADO EST	LADO PV	RUMBO	DISTANCIA	V	COORDENADAS Y	COORDENADAS X
				1	1,320,460.3540	613,331.5726
1	2	N 78°41'57.13" E	1.230	2	1,320,460.5950	613,332.7786
2	3	N 87°20'28.85" E	4.592	3	1,320,460.8080	613,337.3656
3	4	N 89°17'42.60" E	5.121	4	1,320,460.8710	613,342.4866
4	5	S 89°52'18.34" E	8.489	5	1,320,460.8520	613,350.9756
5	6	S 89°54'10.08" E	8.842	6	1,320,460.8370	613,359.8176
6	7	N 87°57'42.81" E	7.564	7	1,320,461.1060	613,367.3766
7	8	N 89°01'05.05" E	8.811	8	1,320,461.2570	613,376.1866
8	9	S 01°31'22.37" W	9.369	9	1,320,451.8910	613,375.9376
9	10	S 88°17'21.89" W	25.426	10	1,320,451.1320	613,350.5226
10	11	S 88°16'19.52" W	6.235	11	1,320,450.9440	613,344.2906
11	12	S 06°27'57.36" W	0.453	12	1,320,450.4940	613,344.2396
12	13	N 88°48'46.11" W	12.790	13	1,320,450.7590	613,331.4521
13	1	N 00°43'10.27" E	9.596	1	1,320,460.3540	613,331.5726

SUPERFICIE: 432.863 m2 = 613.98 Vrs2

ESPACIO PARA ESQUELA

Objeto Lev: Rectificación de área a mayor	Número Catastral: 3051-4-05-036-06010		FIRMA:
Propietario: Juana Mercedes Narvaez Ced: 201-160547-0001J	Ubicación: Bo El Domingazo, de Iglesia Ermita del Socorro 1c al Oeste y 1½c al Norte. Municipio de Granada, Departamento de Granada.		Ejecuta: Ing.Bosco Javier Morgan Lic. Catastral: BMM100426 Cel: 8883-7568 Email: ingmorgan73@gmail.com servicios topograficos
Factor de escala: 1.418415	Área: 432.863 m² = 613.98 Vrs²	Escala: 1 / 400	Fecha: 13 de Junio 2025