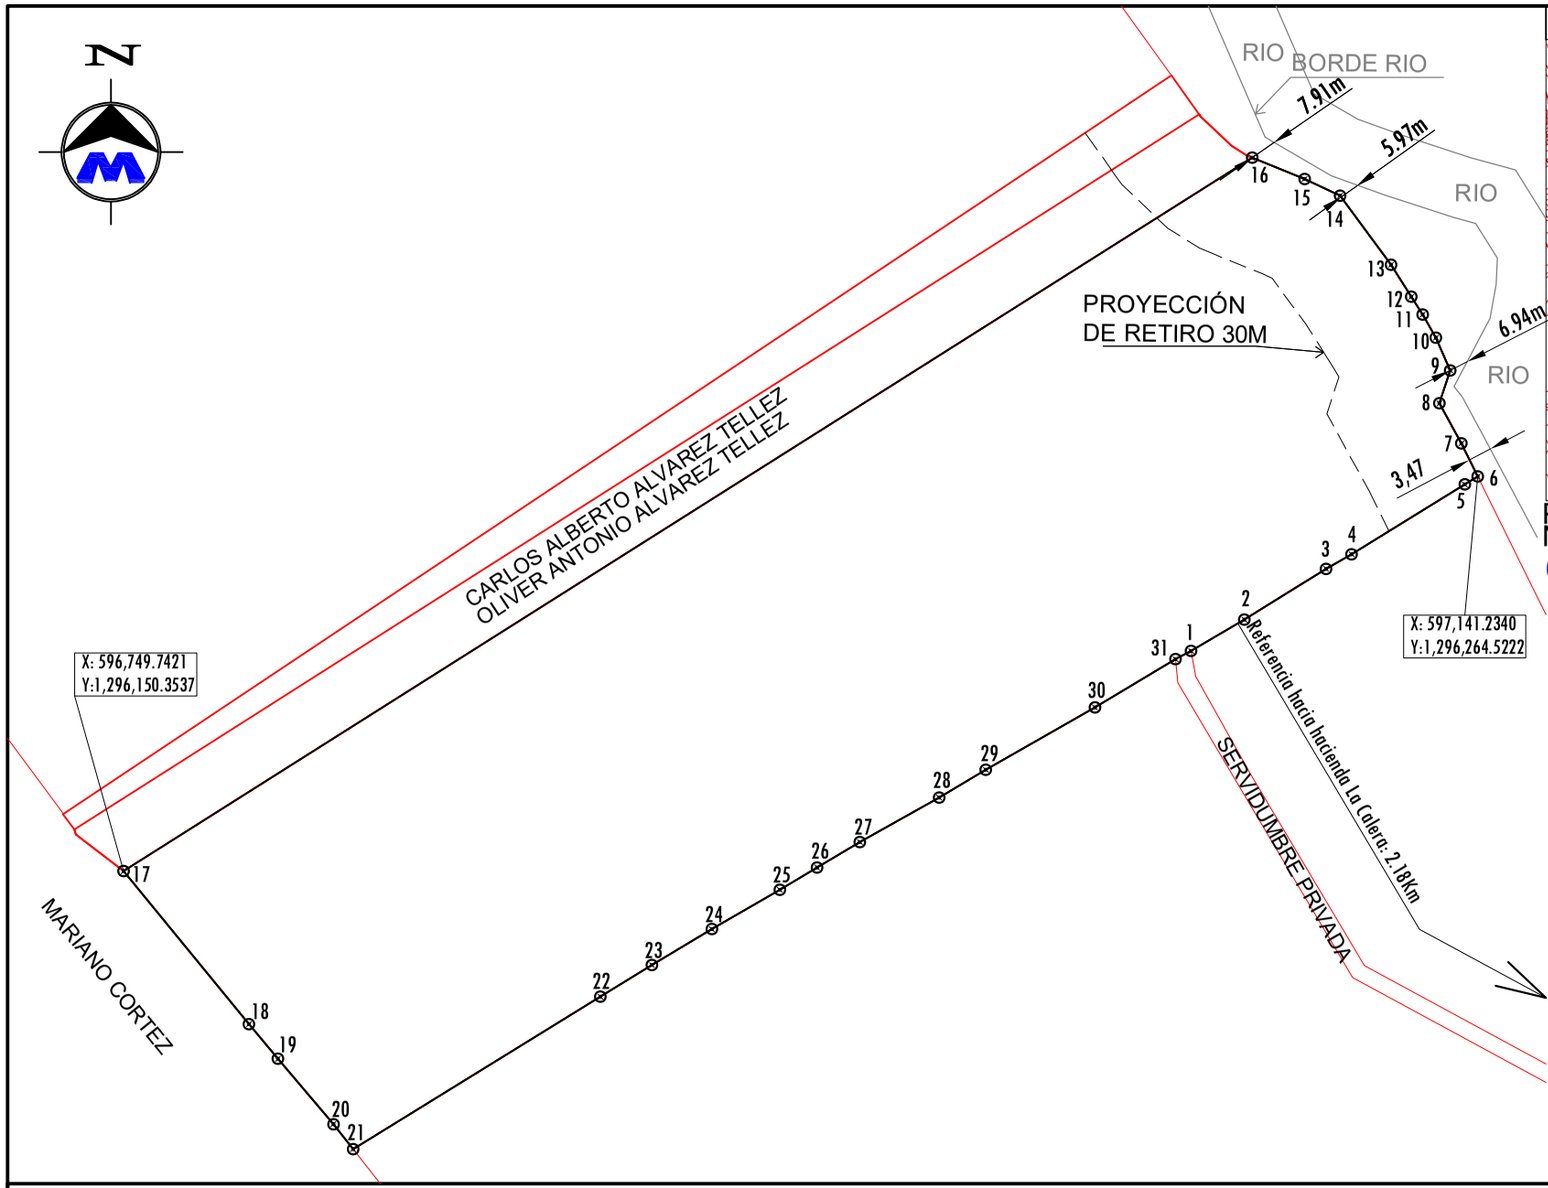

DEPARTAMENTO DE CARAZO MUNICIPIO DE SANTA TEREZA

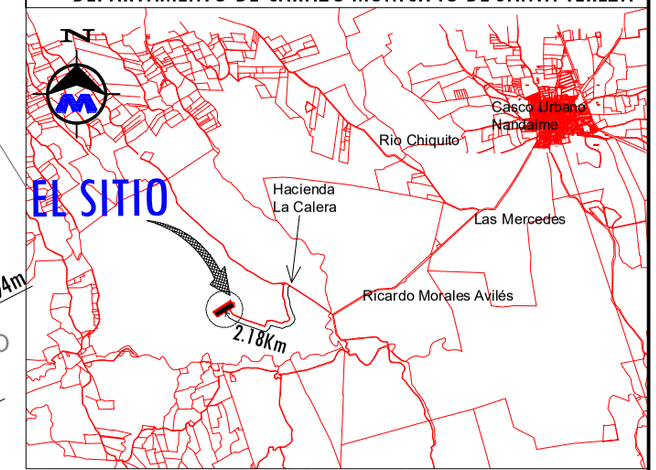

Planta de Ubicacion Sin Escala
Número Catastral:2951-2-11-000-(00200)

COORDENADAS NO VINCULADAS A LA RED GEODESICA DE NICARAGUA

CUADRO DE CONSTRUCCION

LADO EST	LADO PV	RUMBO	DISTANCIA	V	COORDENADAS Y	COORDENADAS X
				1	1,296,214.0507	597,058.3552
1	2	N 59°33'50.74" E	17.863	2	1,296,223.0996	597,073.7565
2	3	N 58°03'29.88" E	27.817	3	1,296,237.8164	597,097.3618
3	4	N 60°23'46.53" E	8.502	4	1,296,242.0165	597,104.7541
4	5	N 58°17'54.29" E	38.446	5	1,296,262.2194	597,137.4634
5	6	N 58°35'10.09" E	4.418	6	1,296,264.5222	597,141.2340
6	7	N 26°16'58.95" W	10.694	7	1,296,274.1108	597,136.4986
7	8	N 28°46'50.88" W	13.210	8	1,296,285.6886	597,130.1387
8	9	N 18°01'27.78" E	10.023	9	1,296,295.2199	597,133.2401
9	10	N 23°29'45.75" W	10.304	10	1,296,304.6696	597,129.1320
10	11	N 29°43'27.97" W	7.711	11	1,296,311.3663	597,125.3085
11	12	N 32°22'39.75" W	6.117	12	1,296,316.5327	597,122.0326
12	13	N 32°25'48.30" W	10.936	13	1,296,325.7629	597,116.1681
13	14	N 36°29'31.37" W	24.835	14	1,296,345.7290	597,101.3983
14	15	N 64°40'32.06" W	11.345	15	1,296,350.5819	597,091.1433
15	16	N 67°51'30.87" W	16.343	16	1,296,356.7414	597,076.0056
16	17	S 57°41'00.15" W	386.062	17	1,296,150.3537	596,749.7421
17	18	S 39°18'46.16" E	55.596	18	1,296,107.3393	596,784.9650
18	19	S 39°41'57.38" E	14.641	19	1,296,096.0742	596,794.3172
19	20	S 40°21'01.99" E	24.819	20	1,296,077.1594	596,810.3869
20	21	S 38°19'48.84" E	9.154	21	1,296,069.9784	596,816.0642
21	22	N 58°22'19.36" E	83.998	22	1,296,114.0269	596,887.5859
22	23	N 58°19'47.14" E	17.467	23	1,296,123.1975	596,902.4516
23	24	N 59°03'42.98" E	20.200	24	1,296,133.5827	596,919.7778
24	25	N 59°49'09.67" E	22.729	25	1,296,145.0092	596,939.4257
25	26	N 59°15'22.87" E	12.553	26	1,296,151.4262	596,950.2146
26	27	N 59°21'29.07" E	14.395	27	1,296,158.7630	596,962.5996
27	28	N 60°33'15.97" E	26.274	28	1,296,171.6790	596,985.4793
28	29	N 59°23'42.57" E	15.713	29	1,296,179.6786	596,999.0033
29	30	N 60°09'19.04" E	36.346	30	1,296,197.7661	597,030.5287
30	31	N 59°11'12.70" E	27.170	31	1,296,211.6838	597,053.8637
31	1	N 62°12'41.57" E	5.077	1	1,296,214.0507	597,058.3552

SUPERFICIE = 42,300.118 m2 = 423 Hectareas = 6 Mnz

Objeto Lev: Venta Total	Número Catastral: 2951-2-11-000-(00200)	Fecha: 16 de Enero del 2025	FIRMA:
Enajenantes: Carlos Alberto Alvarez Tellez, Ced: 001-030297-0006R Oliver Antonio Alvarez Tellez, Ced: 001-300998-0018P	Ubicación: Cmca La Calera, de la hacienda La Calera 2.18 Km sobre acceso Suroeste. Municipio de Santa Tereza. Departamento de Carazo.	Ejecuta: Ing.Bosco Javier Morgan Lic. Catastral: BMM100426 Cel: 8883-7568 Email: ingmorgan73@gmail.com servicios topograficos	
Adquiere: Ana Julia Sandoval Flores, Ced: 321-260794-0006F Armando Josue Traña, Ced: 044-220100-1000G	Area: 42,300.118 m2 = 423 Hectareas = 6 Mnz	Escala: 1 / 2,000	