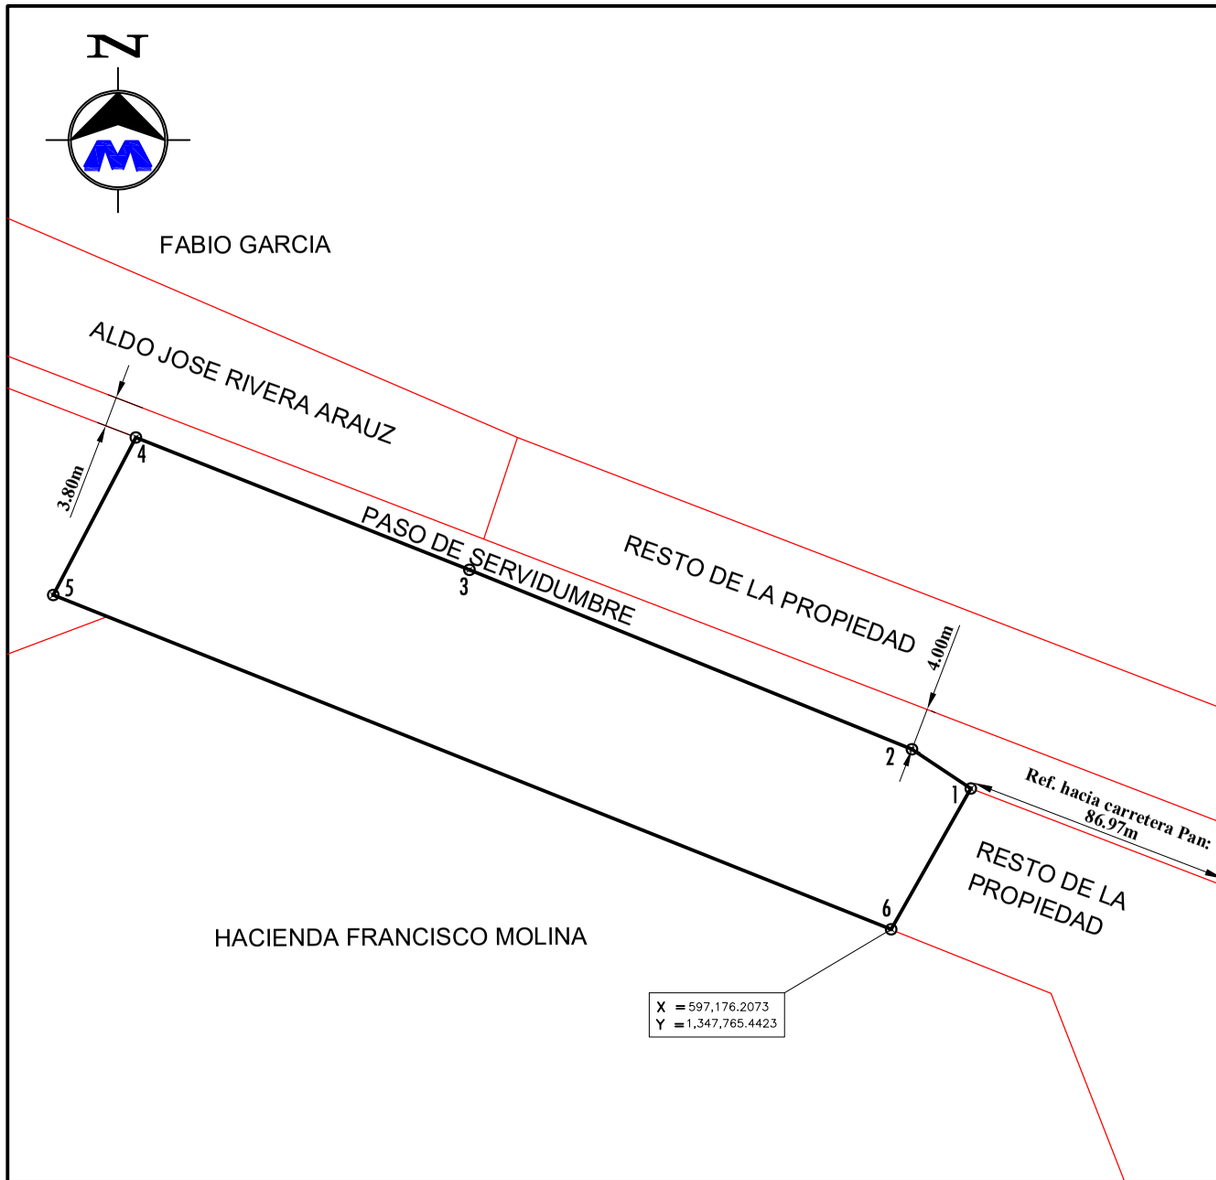

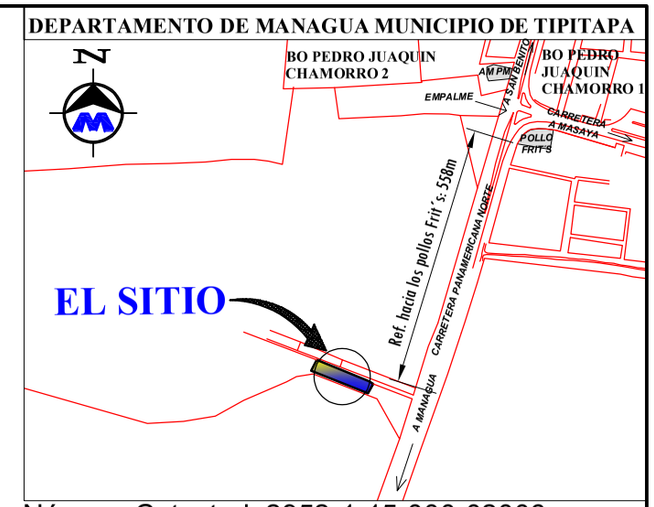

Número Catastral: 2952-1-15-000-02006
Planta de Ubicación Sin Escala

COORDENADAS NO VINCULADAS A LA RED GEODESICA DE NICARAGUA

CUADRO DE CONSTRUCCION

LADO EST	LADO PV	RUMBO	DISTANCIA	V	COORDENADAS Y	COORDENADAS X
				1	1,347,765.4423	597,176.2073
1	2	N 56°21'04.59" W	8.194	2	1,347,769.9829	597,169.3859
2	3	N 67°54'53.40" W	55.236	3	1,347,790.7508	597,118.2027
3	4	N 68°19'42.11" W	41.493	4	1,347,806.0736	597,079.6426
4	5	S 27°40'11.72" W	20.604	5	1,347,787.8262	597,070.0747
5	6	S 68°14'51.33" E	104.348	6	1,347,749.1551	597,166.9929
6	1	N 29°29'55.37" E	18.713	1	1,347,765.4423	597,176.2073

SUPERFICIE: 2,131.753 m2 =3,023.71 Vrs2

Objeto Lev: Venta parcial (Desmembración)	Número Catastral: 2952-1-15-000-02006	FIRMA:
Enajenante: Antonio Moncada Soriano Ced: 081-030958-0005P	Ubicación: De los pollos Frit´s 558 m al Sur, B/d sobre Carretera Panamericana Norte, 86.97m al Oeste B/I Municipio de Tipitapa, Departamento de Managua.	Ejecuta: Ing.Bosco Javier Morgan Lic. Catastral: BMM100426 Cel: 8883-7568 Email: ingmorgan73@gmail.com servicios topograficos
Adquiriente: Aldo José Rivera Arauz Ced: 003-190579-0002Y	Área: 2,131.753 m² = 3,023.71 Vrs² — Escala: 1 / 800	Fecha: 07 de Junio 2025

ESPACIO PARA ESQUELA