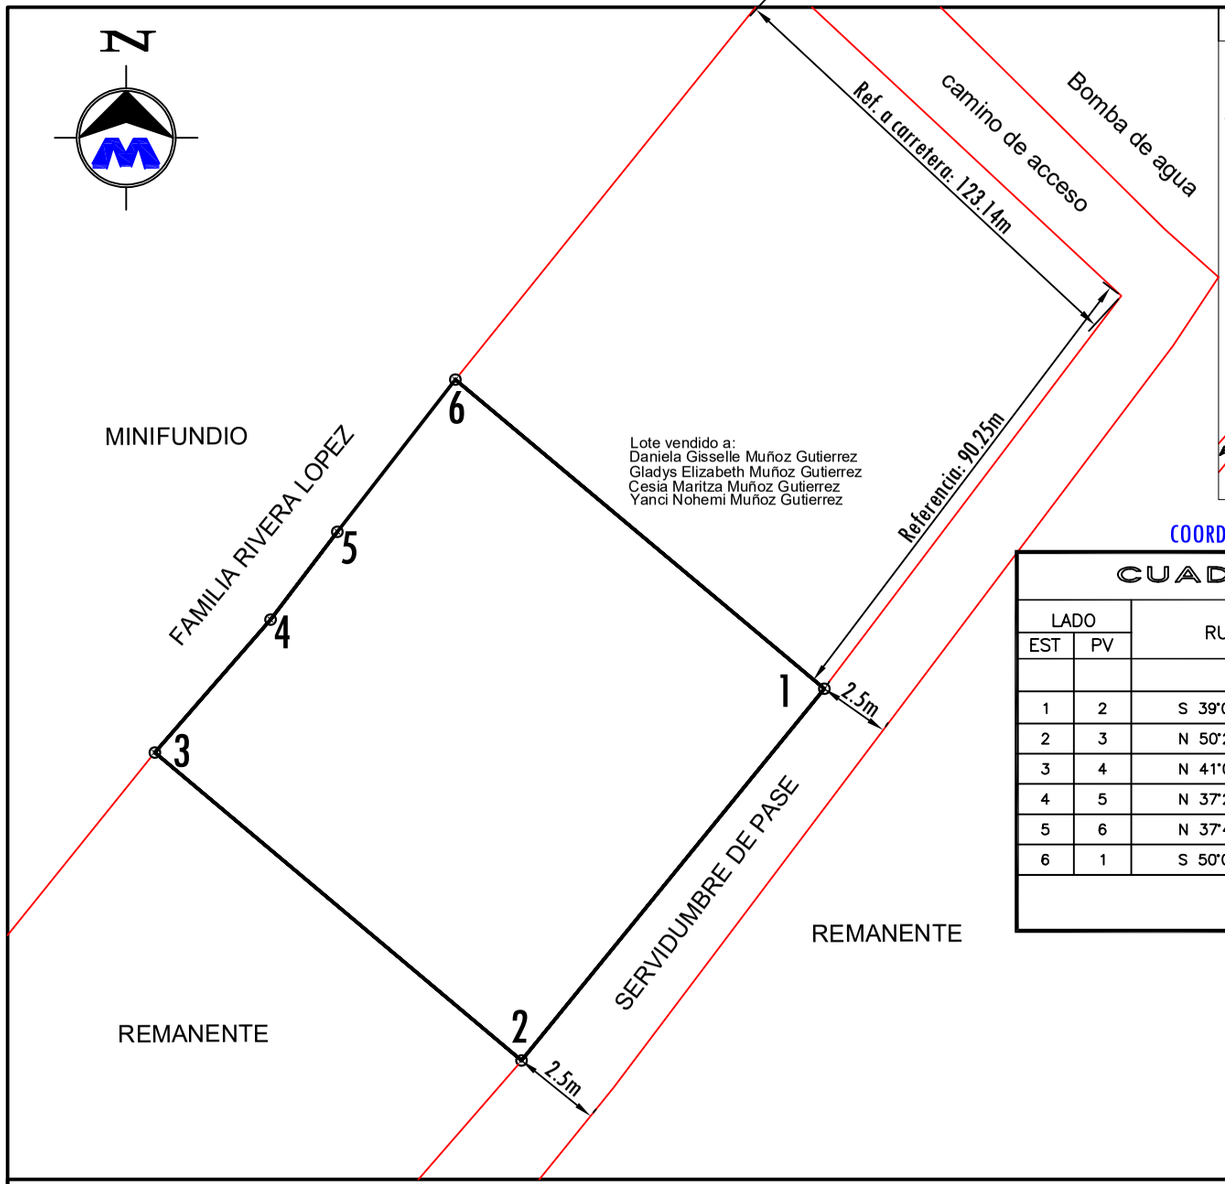

MUNICIPIO DE GRANADA. DEPARTAMENTO DE GRANADA

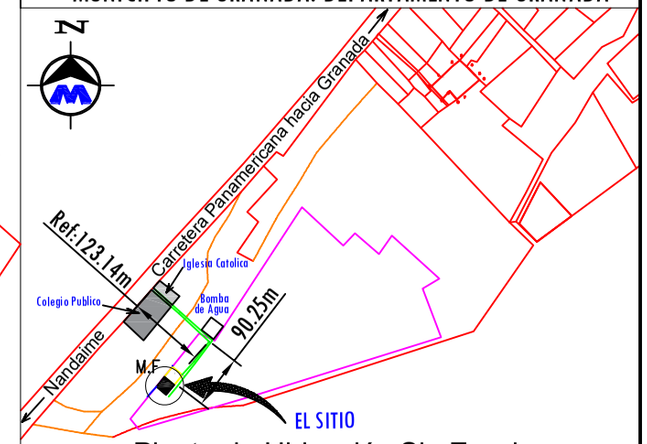

Planta de Ubicación Sin Escala

Número Catastral:3051-4-09-000-02601

COORDENADAS NO VINCULADAS A LA RED GEODESICA DE NICARAGUA

CUADRO DE CONSTRUCCION

LADO EST	LADO PV	RUMBO	DISTANCIA	V	COORDENADAS Y	COORDENADAS X
				1	1,315,179.4500	609,913.9044
1	2	S 39°08'40.05" W	20.914	2	1,315,163.2304	609,900.7022
2	3	N 50°28'26.99" W	20.901	3	1,315,176.5321	609,884.5808
3	4	N 41°00'55.36" E	7.870	4	1,315,182.4703	609,889.7456
4	5	N 37°20'19.90" E	4.820	5	1,315,186.3022	609,892.6688
5	6	N 37°45'35.83" E	8.390	6	1,315,192.9354	609,897.8066
6	1	S 50°02'47.66" E	21.000	1	1,315,179.4500	609,913.9044

SUPERFICIE = 436.811 m2

Objeto Lev:DESMEMBRACION	Número Catastral:3051-4-09-000-02601	Fecha: 27 de Agosto del 2025	FIRMA:
Enajenante: Miguel Angel Gutierrez Urbina Cedula: 201-271256-0002F	Ubicación: Comarca El Hormigon de la escuela publica 123.14m S-E y 90.25m S-O. Municipio de Nandaime. Departamento. Granada.	Ejecuta: Ing.Bosco Javier Morgan Lic. Catastral: BMM100426 Cel: 8883-7568 Email: ingmorgan73@gmail.com SERVICIOS TOPOGRAFICOS	
Adquiriente: Ana Mariela Rivera Garcia Cedula: 201-100793-0006P	Área: 436.811 m² = 619.57 Vrs² / Factor de Escala:1.418415	Escala: 1 / 300	

ESPACIO PARA ESQUELA