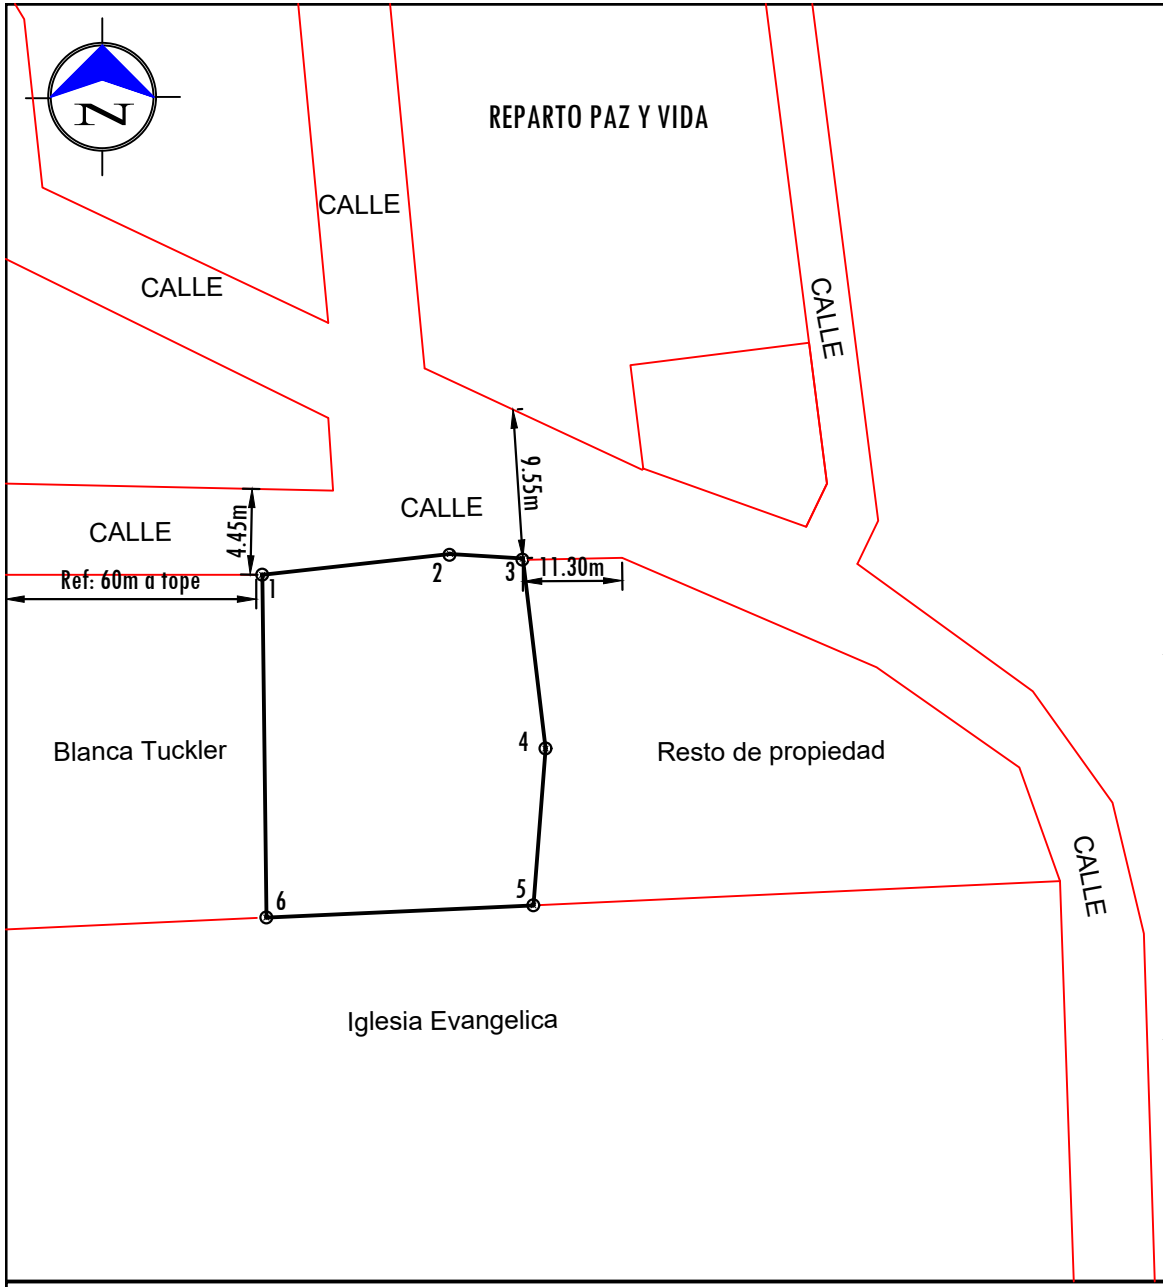

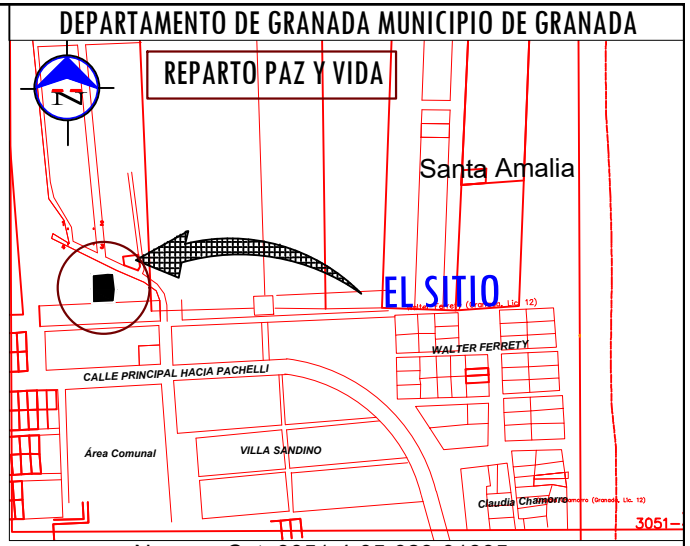

Numero Cat: 3051-4-05-029-01805

Planta de Ubicacion Sin Escala

COORDENADAS NO VINCULADAS A LA RED GEODESICA DE NICARAGUA

CUADRO DE CONSTRUCCION

LADO EST	LADO PV	RUMBO	DISTANCIA	V	COORDENADAS Y	COORDENADAS X
				1	1,321,104.1400	614,398.6800
1	2	N 83°39'35.31" E	12.59	2	1,321,105.5300	614,411.1900
2	3	S 86°20'33.97" E	4.86	3	1,321,105.2200	614,416.0400
3	4	S 06°48'06.21" E	12.75	4	1,321,092.5600	614,417.5500
4	5	S 04°22'39.87" W	10.48	5	1,321,082.1100	614,416.7500
5	6	S 87°23'35.00" W	17.81	6	1,321,081.3000	614,398.9600
6	1	N 00°42'08.51" W	22.84	1	1,321,104.1400	614,398.6800
SUPERFICIE = 422.52 m2						

Objeto Lev: Desmembración - Compra Venta	Numero Cat: 3051-4-05-029-01805	FIRMA:
Enajenante: Jose Luis Peña Delgado Osmani Exequiel Peña Delgado	Ubicacion: Reparto Paz y Vida de la entrada principal 1c norte 11.30m Este ,Municipio de Granada, Departamento de Granada.	Ejecuta: Ing.Bosco Javier Morgan Lic. Catastral: BMM100426 Cel: 8883-7568 Email: ingmorgan73@gmail.com www.morganconstrucciones.com
Adquiriente: Blanca Tuckler	Area: 422.51 m2 = 599.30 vrs2 — Escala: 1 / 500	Fecha: 09 de septiembre del 2024