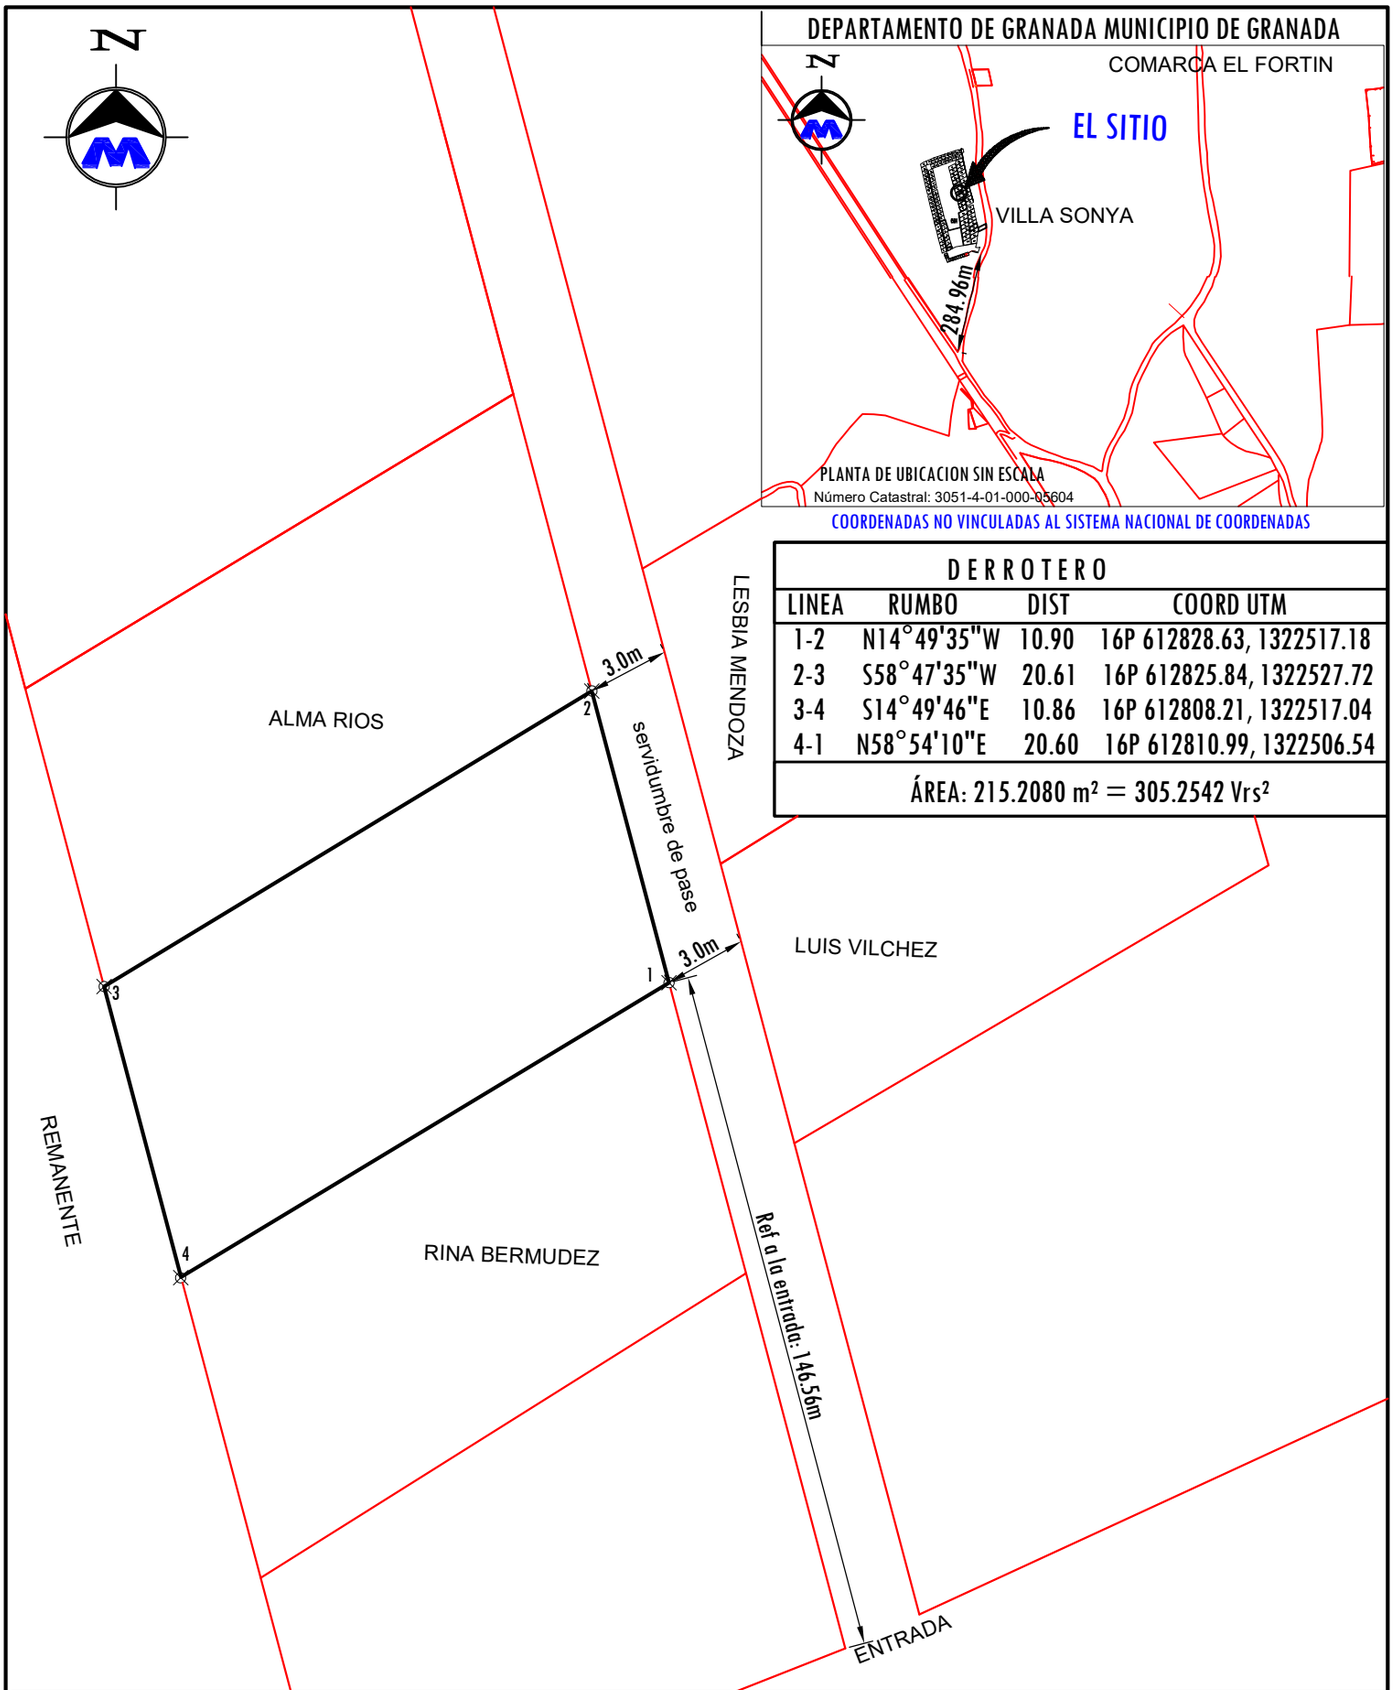

DEPARTAMENTO DE GRANADA MUNICIPIO DE GRANADA

PLANTA DE UBICACION SIN ESCALA
Número Catastral: 3051-4-01-000-05604

COORDENADAS NO VINCULADAS AL SISTEMA NACIONAL DE COORDENADAS

DERROTERO

LINEA	RUMBO	DIST	COORD UTM
1-2	N14°49'35"W	10.90	16P 612828.63, 1322517.18
2-3	S58°47'35"W	20.61	16P 612825.84, 1322527.72
3-4	S14°49'46"E	10.86	16P 612808.21, 1322517.04
4-1	N58°54'10"E	20.60	16P 612810.99, 1322506.54

ÁREA: 215.2080 m² = 305.2542 Vrs²

Objeto Lev: Venta Total	Número Catastral: 3051-4-01-000-05604		FIRMA:
Enajenante: Johanna Auxiliadora Palacios Hernández Cédula: 201-170470-0005J	Ubicacion: Comarca El Fortin. De la entrada principal de Villa Sonya,146.56 m al Noroeste lote # 75. Municipio de Granada. Departamento de Granada.		Ejecuta: Ing.Bosco Javier Morgan Lic. Catastral: BMM100426 SERVICIOS TOPOGRAFICOS
Adquiriente:Bernis Yonin Trejos Cunningham Cédula: 607-300684-0002G	ÁREA: 215.2080 m² = 305.2542 Vrs²	Escala: 1 /250	Fecha: 28 de Abril del 2025

ESPACIO PARA ESQUELA