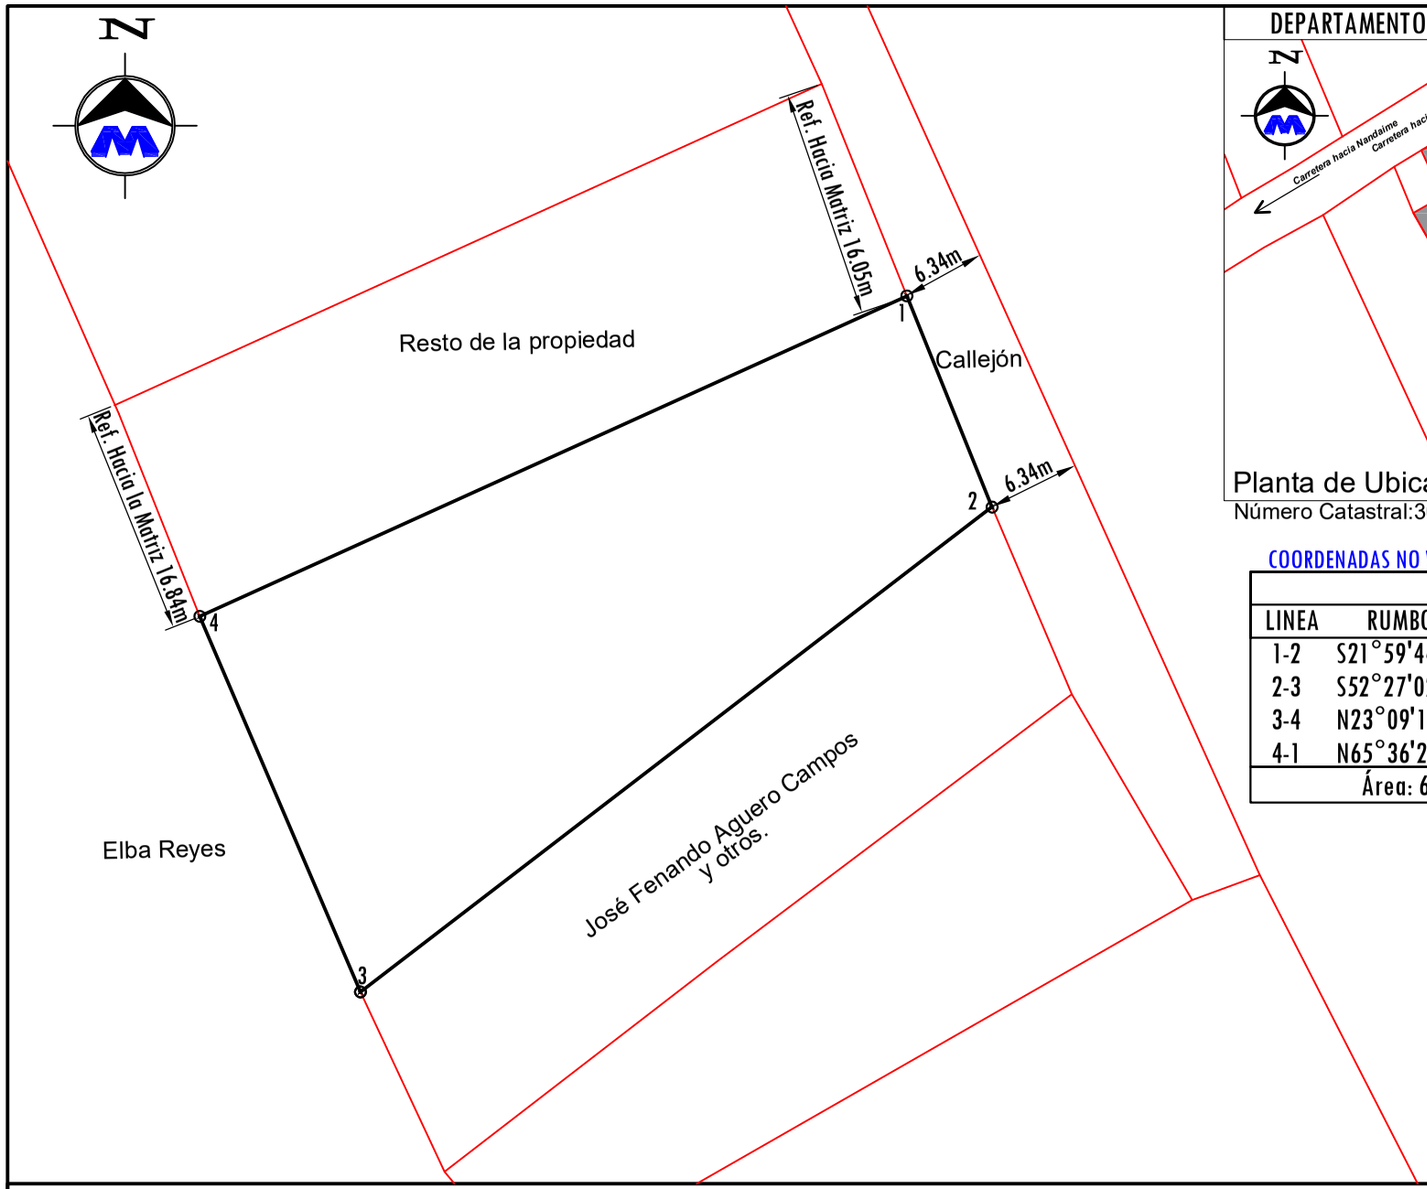

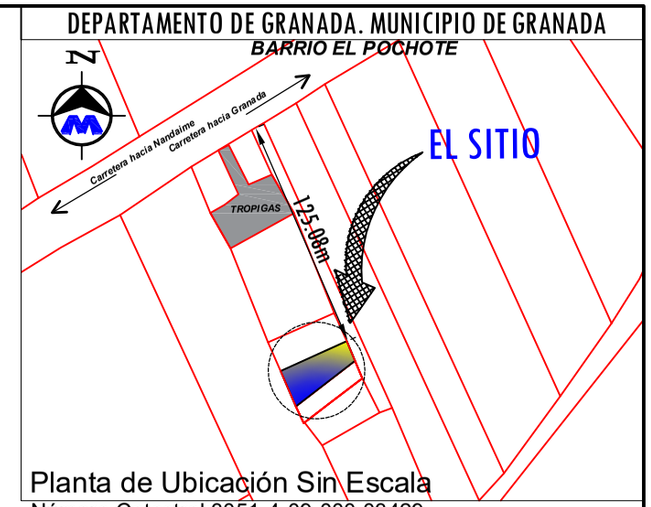

Planta de Ubicación Sin Escala

Número Catastral:3051-4-09-000-03429

COORDENADAS NO VINCULADAS A LA RED GEODESICA DE NICARAGUA

DERROTERO			
LINEA	RUMBO	DIST	COORD UTM
1-2	S21°59'44"E	11.51	16P 611914.53, 1317107.81
2-3	S52°27'02"W	40.30	16P 611918.84, 1317097.14
3-4	N23°09'18"W	20.68	16P 611886.89, 1317072.58
4-1	N65°36'29"E	39.28	16P 611878.76, 1317091.59
Área: 629.3086 m² = 892.6207 Vrs²			

Objeto Lev:Desmembración	Número Catastral: 3051-4-09-000-03429	FIRMA:
Enajenante:Christiane Noe Campos Cabistán Ced:201-010176-0010C	Ubicación: Barrio el Pochote, Planta Tropigas 125.08 m al Sur. Municipio de Granada, Departamento de Granada.	Ejecuta: Ing.Bosco Javier Morgan Lic. Catastral: BMM100426 Cel: 8883-7568 Email: ingmorgan73@gmail.com SERVICIOS TOPOGRAFICOS
Adquirientes: Gregorio de Jesus Campos Vega Ced: 201-090101-1007L Marco Antonio Campos Vega Ced: 201-131296-0007N Dina Raquel Campos Vega Ced: 201-260799-1001X Marco Antonio Campos Cabistan Ced: 201-250472-0008T	Área: 629.3086 m² = 892.6207 Vrs² Escala: 1 / 350	Fecha: 2 de Mayo del 2025

ESPACIO PARA ESQUELA