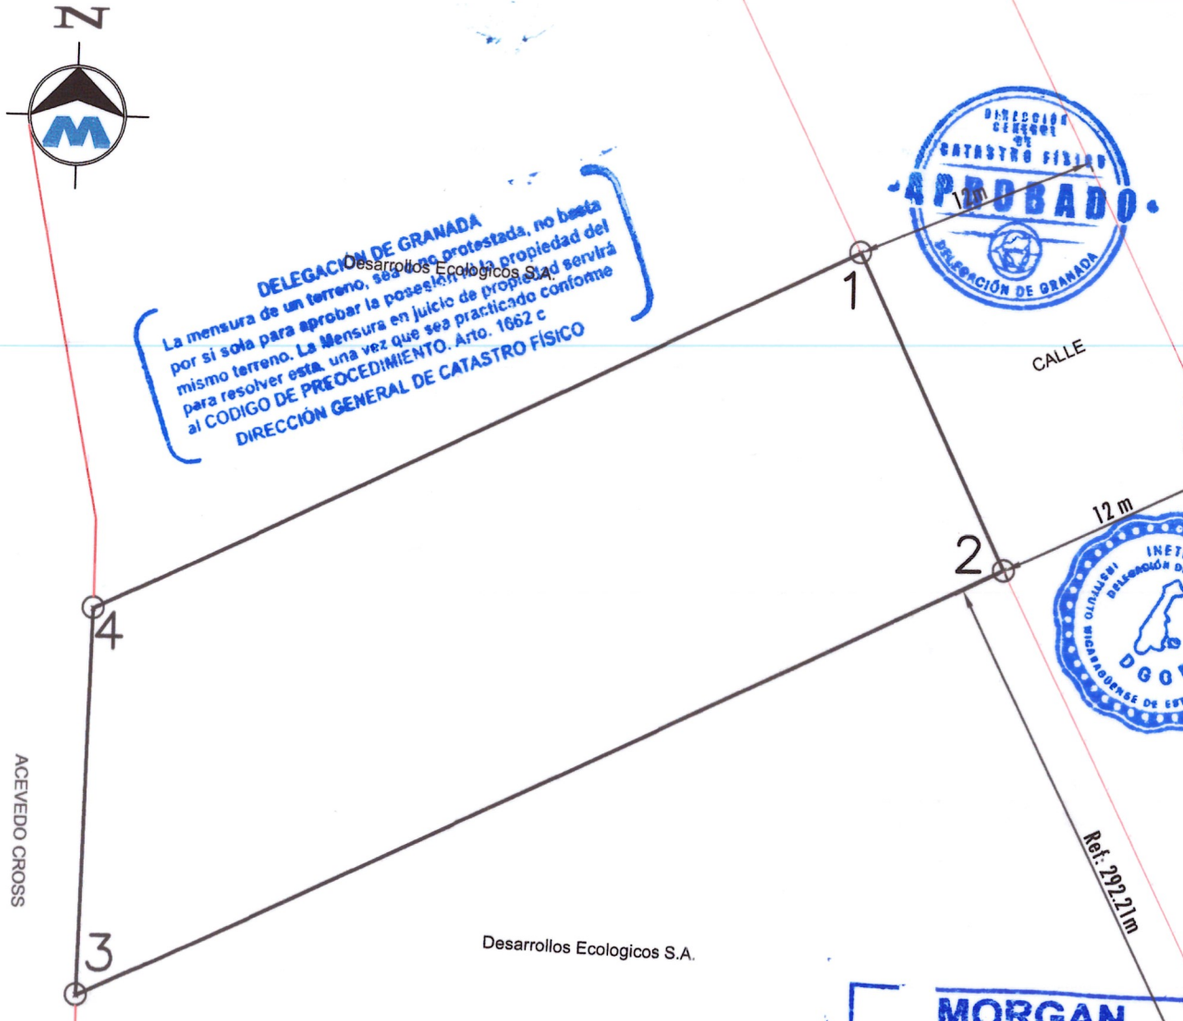

DELEGACION DE GRANADA
La mensura de un terreno, sea no protestada, no basta por si sola para aprobar la posesión de la propiedad del mismo terreno. La Mensura en juicio de propiedad servirá para resolver esta, una vez que sea practicado conforme al CODIGO DE PROCEDIMIENTO. Arto. 1662 c
DIRECCIÓN GENERAL DE CATASTRO FÍSICO

DIRECCIÓN GENERAL DE CATASTRO FÍSICO
APROBADO
DELEGACIÓN DE GRANADA

INETER
DELEGACIÓN DE GRANADA
DGCF
INSTITUTO NICARAGÜENSE DE ESTUDIOS TERRITORIALES

MORGAN
Servicios Topograficos
Ing Bosco Javier Morgan
Lic Catastral: BMM100426
Cel: 8883 7568 T

DEPARTAMENTO DE GRANADA MUNICIPIO DE GRANADA

Planta de Ubicacion Sin Escala

Número Catastral: 6301-8922-4883-12

COORDENADAS NO VINCULADAS A LA RED GEODESICA DE NICARAGUA

CUADRO DE CONSTRUCCION

LADO EST	LADO PV	RUMBO	DISTANCIA	V	COORDENADAS Y	COORDENADAS X
				1	1,319,297.3693	608,282.7746
1	2	S 25°39'52.70" E	25.009	2	1,319,274.8276	608,293.6061
2	3	S 64°31'25.11" W	73.600	3	1,319,243.1694	608,227.1627
3	4	N 01°13'08.96" E	27.717	4	1,319,270.8798	608,227.7525
4	1	N 64°17'32.10" E	61.067	1	1,319,297.3693	608,282.7746

SUPERFICIE = 1,674.858 m2

Transacción	Cudoc	Objeto Plano	Área (m²)	No. Lote
T-4CIDFS-001	0042532	TRASPASO TOTAL	1,674.86	
Parcela Objeto	6301892488312		Documento	W8BZXAC
No. Licencia: BMM100426	Fecha Aprobación: 26/2/2026		Fecha Vencimiento: 26/2/2027 14:35:17	

Adquiriente: Benjamin Matthias Michael Hass
Pasaporte # C74NHC6CV
Tilmann Mathias Bohme Pasaporte # C3JCPZNCY
Martha Lorena Alonzo Salmeron Cedula:401-290785-0000V

Objeto Lev: VENTA TOTAL	Número Catastral: 6301-8922-4883-12		FIRMA:
Enajenante: Brian Edbrooke Davis Pasaporte # 641338019 Nancy Finn Davis conocida como Nancy Finn Chally Pasaporte # 655073411	Ubicación: Comarca La Laguna de la primera entrada del Reparto Silvia Ferrufino 3,579.73m al Oeste y 292.21m al Noroeste. Vistalagos. Municipio de Granada. Depto de Granada.		Ejecuta: Ing.Bosco Javier Morgan Lic. Catastral: BMM100426 Cel: 8883-7568 Email: ingmorgan73@gmail.com servicios topograficos
Adquiriente: Arriba reflejados	Área: 1,674.858 m2= 2,375.64vrs2	Escala: 1 / 500	Fecha: 19 de Febrero del 2026

SELLO

Objeto Lev: Venta Total

COORDENADAS NO VINCULADAS A LA RED GEODESICA DE NICARAGUA

CUADRO DE CONSTRUCCION

LADO		RUMBO	DISTANCIA	V	COORDENADAS	
EST	PV				Y	X
				1	1,319,297.3693	608,282.7746
1	2	S 25°39'52.70" E	25.009	2	1,319,274.8276	608,293.6061
2	3	S 64°31'25.11" W	73.600	3	1,319,243.1694	608,227.1627
3	4	N 01°13'08.96" E	27.717	4	1,319,270.8798	608,227.7525
4	1	N 64°17'32.10" E	61.067	1	1,319,297.3693	608,282.7746

SUPERFICIE = 1,674.858 m2

MORGAN
Servicios Topograficos
Ing Bosco Javier Morgan
Lic Catastral BMM100426
Cel: 8883 7568

Ejecuta: Ing.Bosco Javier Morgan
Lic. Catastral: BMM100426
Cel: 8883-7568 Email: ingmorgan73@gmail.com
servicios topograficos