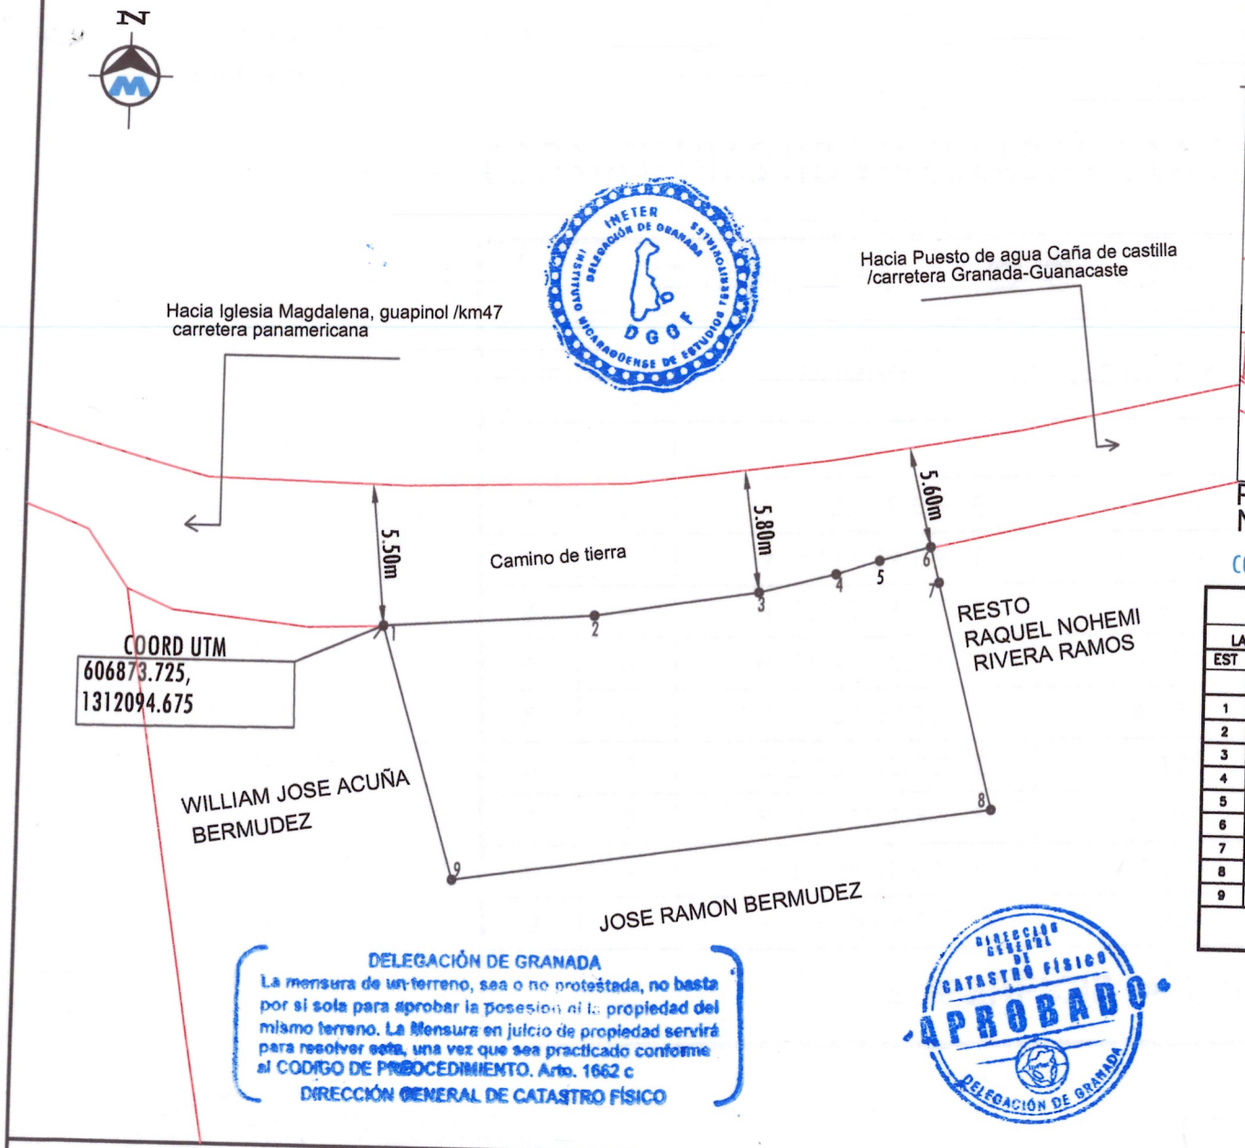

INETER
DELEGACIÓN DE GRANADA
INSTITUTO NICARAGÜENSE DE ESTUDIOS TERRITORIALES
DGOT

DELEGACIÓN DE GRANADA
La mensura de un terreno, sea o no protestada, no basta por si sola para aprobar la posesion ni la propiedad del mismo terreno. La Mensura en juicio de propiedad servirá para resolver esta, una vez que sea practicado conforme al CODIGO DE PROCEDIMIENTO. Arto. 1662 c
DIRECCIÓN GENERAL DE CATASTRO FÍSICO

DIRECCIÓN GENERAL DE CATASTRO FÍSICO
APROBADO
DELEGACIÓN DE GRANADA

DEPARTAMENTO DE GRANADA MUNICIPIO DE DIRIOMO

Planta de Ubicacion Sin Escala
Número Catastral:63016290280613

COORDENADAS NO VINCULADAS A LA RED GEODESICA DE NICARAGUA

CUADRO DE CONSTRUCCION

LADO EST	LADO PV	RUMBO	DISTANCIA	V	COORDENADAS Y	COORDENADAS X
				1	1,312,094.6755	606,873.7259
1	2	S 87°00'09.62" E	18.475	2	1,312,093.7094	606,892.1758
2	3	N 87°41'29.88" E	14.574	3	1,312,094.2965	606,906.7385
3	4	N 82°30'24.35" E	6.872	4	1,312,095.1926	606,913.5515
4	5	N 78°49'05.66" E	4.023	5	1,312,095.9727	606,917.4978
5	6	N 81°03'37.59" E	4.639	6	1,312,096.6935	606,922.0801
6	7	S 07°30'18.72" E	3.170	7	1,312,093.5504	606,922.4942
7	8	S 07°09'12.37" E	20.293	8	1,312,073.4152	606,925.0212
8	9	S 88°24'12.03" W	47.500	9	1,312,072.0917	606,877.5394
9	1	N 09°35'04.50" W	22.904	1	1,312,094.6755	606,873.7259

SUPERFICIE = 1,048.802 m2

MORGAN
Servicios Topograficos
Ing Bosco Javier Morgan
Lic Catastral: BMM100426
Cel: 8883-7568

Objeto Lev: Venta Parcial -Desmembracion	Número Catastral:63016290280613	Fecha: 25 de Febrero del 2026	FIRMA:
Enajenante: Raquel Nohemi Rivera Ramos Cédula: 201-111189-0002K	Ubicación: Comarca caña de castilla, Sector los Bermudez, De la Iglesia Magdalena el Guapinol 885m al Este, M/D. Municipio de Diriomo. Dpto. Granada	Ejecuta: Ing.Bosco Javier Morgan Lic. Catastral: BMM100426 Cel: 8883-7568 Email: ingmorgan73@gmail.com servicios topograficos	
Adquiere: Rosa Esmeralda Castillo Castro Cédula: 202-221171-0002Y	Area: 1048.802 m2 = 1487.636vrs2	Escala: 1 / 600	

Transacción	Cudoc	Objeto Plano	Área (m²)	No. Lote
T-4CIL9I-001	0042698	DESMEMBRACIÓN	1,048.80	
Parcela Objeto	63016290081414		Documento	W8BZZ33
No. Licencia: BMM100426	Fecha Aprobación: 3/3/2026		Fecha Vencimiento: 3/3/2027	

Objeto Lev: Venta Parcial -Desmembracion

Numero Catastral:63016290280613

Fecha: 25 de Febrero del 2026

COORDENADAS NO VINCULADAS A LA RED GEODESICA DE NICARAGUA

CUADRO DE CONSTRUCCION

LADO		RUMBO	DISTANCIA	V	COORDENADAS	
EST	PV				Y	X
				1	1,312,094.6755	606,873.7259
1	2	S 87°00'09.62" E	18.475	2	1,312,093.7094	606,892.1758
2	3	N 87°41'29.88" E	14.574	3	1,312,094.2965	606,906.7385
3	4	N 82°30'24.35" E	6.872	4	1,312,095.1926	606,913.5515
4	5	N 78°49'05.66" E	4.023	5	1,312,095.9727	606,917.4978
5	6	N 81°03'37.59" E	4.639	6	1,312,096.6935	606,922.0801
6	7	S 07°30'18.72" E	3.170	7	1,312,093.5504	606,922.4942
7	8	S 07°09'12.37" E	20.293	8	1,312,073.4152	606,925.0212
8	9	S 88°24'12.03" W	47.500	9	1,312,072.0917	606,877.5394
9	1	N 09°35'04.50" W	22.904	1	1,312,094.6755	606,873.7259

SUPERFICIE = 1,048.802 m2

Ejecuta: Ing.Bosco Javier Morgan
Lic. Catastral: BMM100426
Cel: 8883-7568 Email: ingmorgan73@gmail.com
servicios topograficos

MORGAN
Servicios Topograficos
Ing Bosco Javier Morgan
Lic Catastral BMM100426
Cel 8883 7568 T