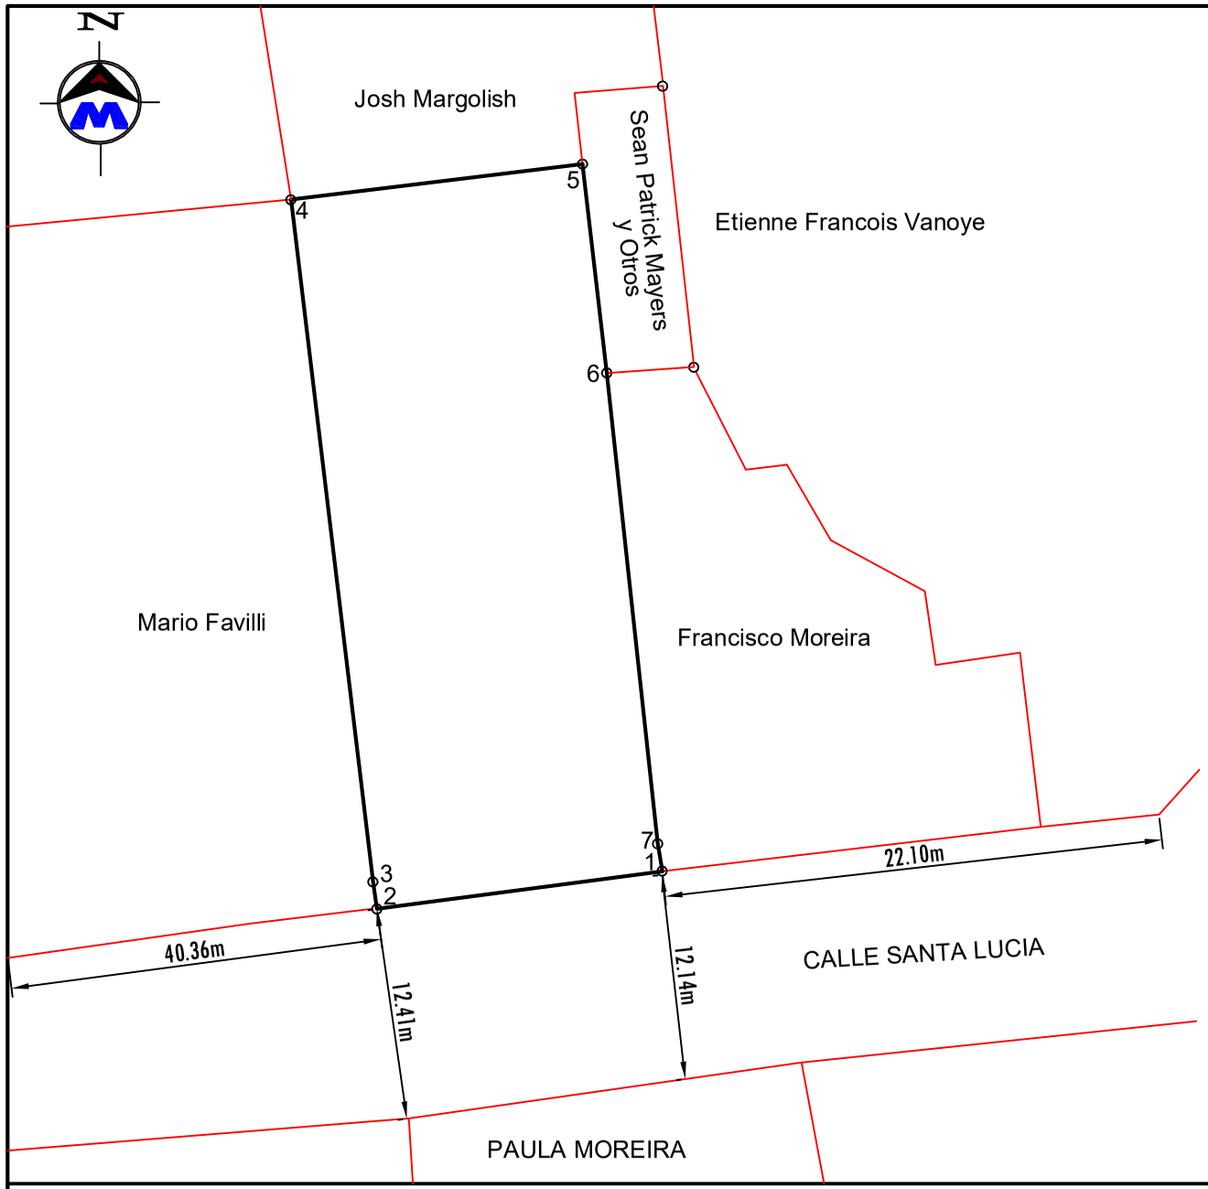

MUNICIPIO DE GRANADA. DEPARTAMENTO DE GRANADA

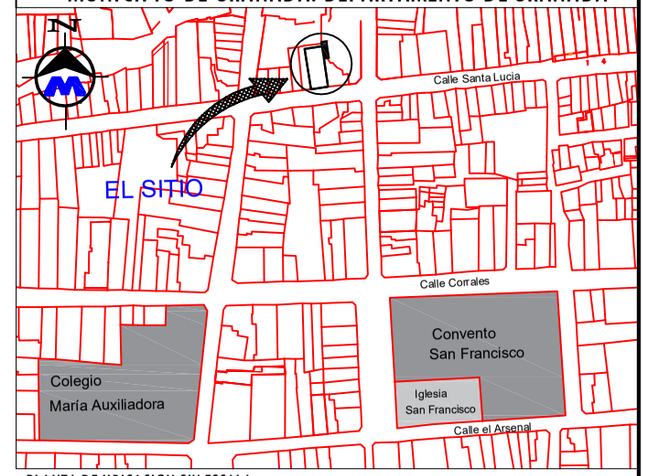

PLANTA DE UBICACION SIN ESCALA

Número Catastral: 3051-4-05-068-06650

COORDENADAS NO VINCULADAS A LA RED GEODESICA DE NICARAGUA

DERROTERO

LINEA	RUMBO	DIST	COORD UTM
1-2	S82°28'19"W	12.52	16P 614025.76, 1319469.66
2-3	N07°11'03"W	1.20	16P 614013.35, 1319468.02
3-4	N06°51'04"W	29.84	16P 614013.20, 1319469.21
4-5	N83°06'13"E	12.74	16P 614009.64, 1319498.84
5-6	S06°36'13"E	9.13	16P 614022.29, 1319500.37
6-7	S06°11'55"E	20.56	16P 614023.34, 1319491.30
7-1	S09°27'44"E	1.22	16P 614025.56, 1319470.86

Área: 390.9551 m² = 554.5366 Vrs²

Enajenantes:
Sean Patrick Mayers. Pasaporte # 526331807
Eloisa Magdalena Mayers. pasaporte #143922027
Arantxa Julietta Mayers. Pasaporte # 129465647
Mohini Maria Natarajan Mayers Pasaporte # 132523237

ESPACIO PARA ESQUELA

Objeto: Verificación de área	Número Catastral: 3051-4-05-068-06650		FIRMA:
Propietarios: Arriba reflejados	Ubicación: Calle Santa Lucia del Parque Central 3c al norte 52.85 m al Este, 72.51m norte. Municipio de Granada. Dpto Granada.		Ejecuta: Ing.Bosco Javier Morgan Lic. Catastral: BMM100426 Cel: 8883-7568 Email: ingmorgan73@gmail.com www.morganconstrucciones.com
Factor de escala: 1.418415	Área: 390.9551 m² = 554.5366 Vrs²	Escala: 1: 300	Fecha:14 de Mayo del 2025